Tél.
e-mail contact@bet-structuro.com

HOUILLES

Objet

CONSTRUCTION D'UNE MAISON INDIVIDUELLE

Partie d'ouvrage

Maître d'ouvrage M. Pedro Navarro Arce

Dessin		échelle
2	Coffrages - 1	1/50

Ingénieur des structures	Conducteur des travaux
BET STRUCTURO	

Date	Révision	Mise à jour	Protocole
07/04/2026			

Ce projet est protégé par la loi.

LÉGENDE HACHURES
Légende Hachures

LÉGENDE HACHURES
Légende Hachures

	Description
Béton armé	
	Poteau qui commence
	Poteau qui passe
	Poteau qui termine

DISPOSITIONS CONSTRUCTIVES

Béton vibré, classe min C25/30
Enrobage min = 3 cm

2 ou 4 Equerres d'angle horizontaux 60×60 – ø 10 mm à prévoir au niveau des fondations, à chaque intersection de semelle


Intersection en L — Intersection en T

2 ou 4 Equerres d'angle horizontaux 60×60 – ø 10 mm à prévoir au niveau des fondations, à chaque intersection de chainage horizontal


Intersection en L — Intersection en T

4 Equerres verticaux 60×60 – ø 10 mm, à prévoir au niveau des fondations, à chaque poteau ou chainage vertical

U verticaux 16cm×H – ø 10 mm – espace. = 16.5 cm ancrés dans la fondation à prévoir au niveau des murs de soubassement

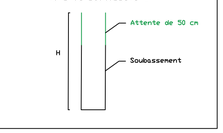

TOITURE

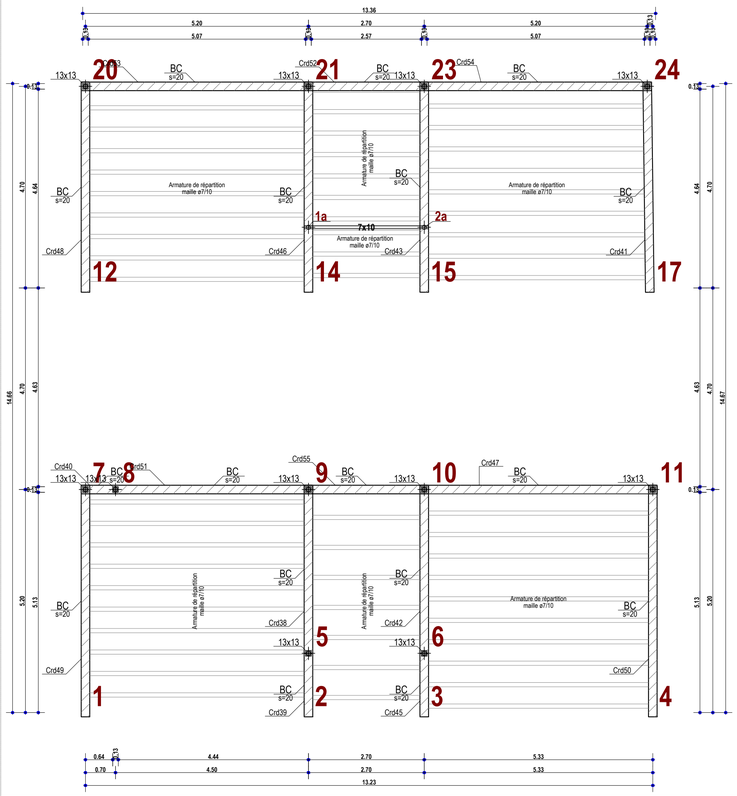

LÉGENDE
MAÇONNERIES :
BC BRIQUE EN TERRE CREUSE
C25/30 Btn C25/30_B500B


CHAINAGE

Id	Mtr	Htr	Base	Lngr	Arm long	Cadres
Crd87	Btn C25/30_B500B	0.13	0.20	5.40	4ø10	ø6/15
Crd68	Btn C25/30_B500B	0.13	0.20	1.58	4ø10	ø6/15
Crd85	Btn C25/30_B500B	0.13	0.20	2.90	4ø10	ø6/15
Crd66	Btn C25/30_B500B	0.13	0.20	1.58	4ø10	ø6/15
Crd69	Btn C25/30_B500B	0.13	0.20	5.53	4ø10	ø6/15
Crd72	Btn C25/30_B500B	0.13	0.20	5.40	4ø10	ø6/15
Crd73	Btn C25/30_B500B	0.13	0.20	5.40	4ø10	ø6/15
Crd70	Btn C25/30_B500B	0.13	0.20	5.53	4ø10	ø6/15
Crd71	Btn C25/30_B500B	0.13	0.20	3.42	4ø10	ø6/15
Crd58	Btn C25/30_B500B	0.13	0.20	4.90	4ø10	ø6/15
Crd59	Btn C25/30_B500B	0.13	0.20	4.80	4ø10	ø6/15
Crd56	Btn C25/30_B500B	0.13	0.20	4.90	4ø10	ø6/15
Crd57	Btn C25/30_B500B	0.13	0.20	3.92	4ø10	ø6/15
Crd60	Btn C25/30_B500B	0.13	0.20	5.30	4ø10	ø6/15
Crd83	Btn C25/30_B500B	0.13	0.20	2.70	4ø10	ø6/15
Crd64	Btn C25/30_B500B	0.13	0.20	2.70	4ø10	ø6/15
Crd81	Btn C25/30_B500B	0.13	0.20	4.80	4ø10	ø6/15
Crd82	Btn C25/30_B500B	0.13	0.20	0.80	4ø10	ø6/15
Crd37	Btn C25/30_B500B	0.13	0.20	5.30	4ø10	ø6/15
Crd12	Btn C25/30_B500B	0.13	0.20	4.50	4ø10	ø6/15
Crd13	Btn C25/30_B500B	0.13	0.20	0.80	4ø10	ø6/15
Crd10	Btn C25/30_B500B	0.13	0.20	4.02	4ø10	ø6/15
Crd11	Btn C25/30_B500B	0.13	0.20	3.42	4ø10	ø6/15
Crd14	Btn C25/30_B500B	0.13	0.20	2.85	4ø10	ø6/15
Crd77	Btn C25/30_B500B	0.13	0.20	2.01	4ø10	ø6/15

Id: Identifiant chaînage
Mtr: matériau
Htr: hauteur (en m)
Base: base (en m)
Lngr: longueur (en m)
Arm long: armatures longitudinales (nombre/diamètre en mm)
Cadres: armatures des cadres (diamètre en mm/espacement en cm)

Échelle: 1/50

PH R+1

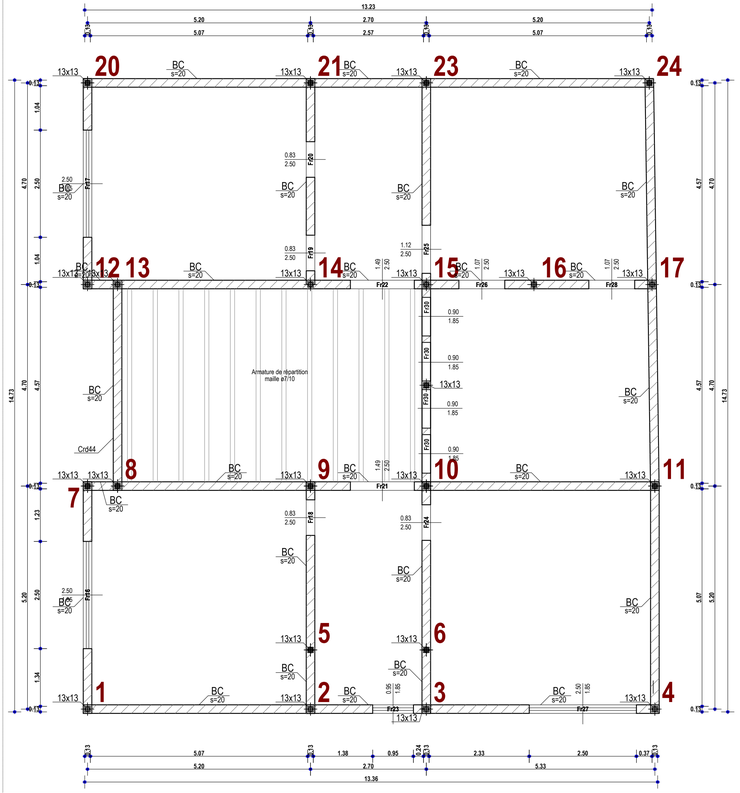

LÉGENDE
MAÇONNERIES :
BC BRIQUE EN TERRE CREUSE
C25/30 Btn C25/30_B500B


CHAINAGE

Id	Mtr	Htr	Base	Lngr	Arm long	Cadres
Crd44	Btn C25/30_B500B	0.13	0.20	4.90	4ø10	ø6/20

Id: Identifiant chaînage
Mtr: matériau
Htr: hauteur (en m)
Base: base (en m)
Lngr: longueur (en m)
Arm long: armatures longitudinales (nombre/diamètre en mm)
Cadres: armatures des cadres (diamètre en mm/espacement en cm)

Échelle: 1/50

PH RDC

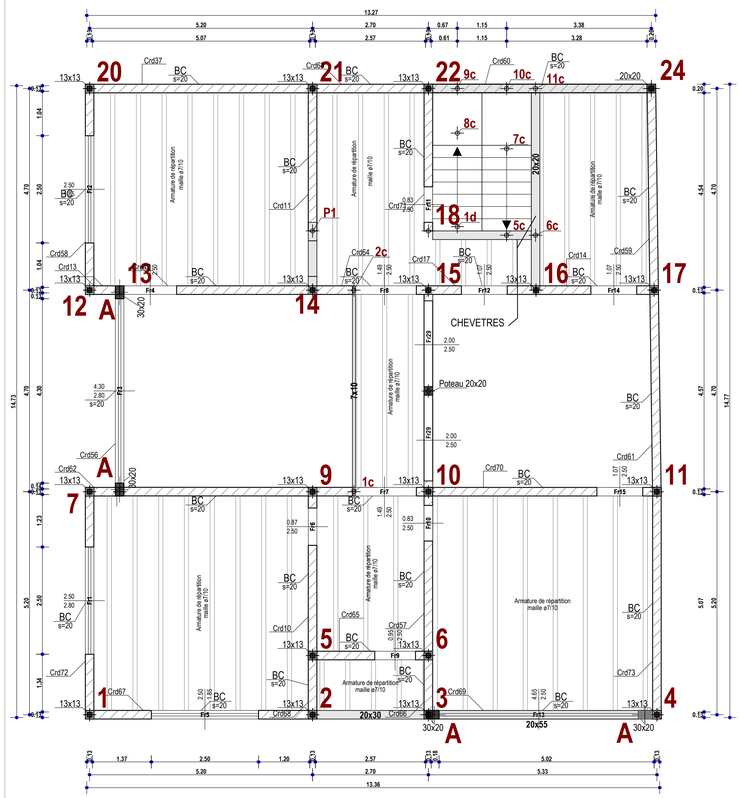


LÉGENDE
MAÇONNERIES :
BC BRIQUE EN TERRE CREUSE
C25/30 Btn C25/30_B500B

CHAINAGE

Id	Mtr	Htr	Base	Lngr	Arm long	Cadres
Crd87	Btn C25/30_B500B	0.13	0.20	5.40	4ø10	ø6/15
Crd68	Btn C25/30_B500B	0.13	0.20	1.58	4ø10	ø6/15
Crd85	Btn C25/30_B500B	0.13	0.20	2.90	4ø10	ø6/15
Crd66	Btn C25/30_B500B	0.13	0.20	1.58	4ø10	ø6/15
Crd69	Btn C25/30_B500B	0.13	0.20	5.53	4ø10	ø6/15
Crd72	Btn C25/30_B500B	0.13	0.20	5.40	4ø10	ø6/15
Crd73	Btn C25/30_B500B	0.13	0.20	5.40	4ø10	ø6/15
Crd70	Btn C25/30_B500B	0.13	0.20	5.53	4ø10	ø6/15
Crd71	Btn C25/30_B500B	0.13	0.20	3.42	4ø10	ø6/15
Crd58	Btn C25/30_B500B	0.13	0.20	4.90	4ø10	ø6/15
Crd59	Btn C25/30_B500B	0.13	0.20	4.80	4ø10	ø6/15
Crd56	Btn C25/30_B500B	0.13	0.20	4.90	4ø10	ø6/15
Crd57	Btn C25/30_B500B	0.13	0.20	3.92	4ø10	ø6/15
Crd60	Btn C25/30_B500B	0.13	0.20	5.30	4ø10	ø6/15
Crd83	Btn C25/30_B500B	0.13	0.20	2.70	4ø10	ø6/15
Crd64	Btn C25/30_B500B	0.13	0.20	2.70	4ø10	ø6/15
Crd81	Btn C25/30_B500B	0.13	0.20	4.80	4ø10	ø6/15
Crd82	Btn C25/30_B500B	0.13	0.20	0.80	4ø10	ø6/15
Crd37	Btn C25/30_B500B	0.13	0.20	5.30	4ø10	ø6/15
Crd12	Btn C25/30_B500B	0.13	0.20	4.50	4ø10	ø6/15
Crd13	Btn C25/30_B500B	0.13	0.20	0.80	4ø10	ø6/15
Crd10	Btn C25/30_B500B	0.13	0.20	4.02	4ø10	ø6/15
Crd11	Btn C25/30_B500B	0.13	0.20	3.42	4ø10	ø6/15
Crd14	Btn C25/30_B500B	0.13	0.20	2.85	4ø10	ø6/15
Crd77	Btn C25/30_B500B	0.13	0.20	2.01	4ø10	ø6/15

Id: Identifiant chaînage
Mtr: matériau
Htr: hauteur (en m)
Base: base (en m)
Lngr: longueur (en m)
Arm long: armatures longitudinales (nombre/diamètre en mm)
Cadres: armatures des cadres (diamètre en mm/espacement en cm)

PH VS

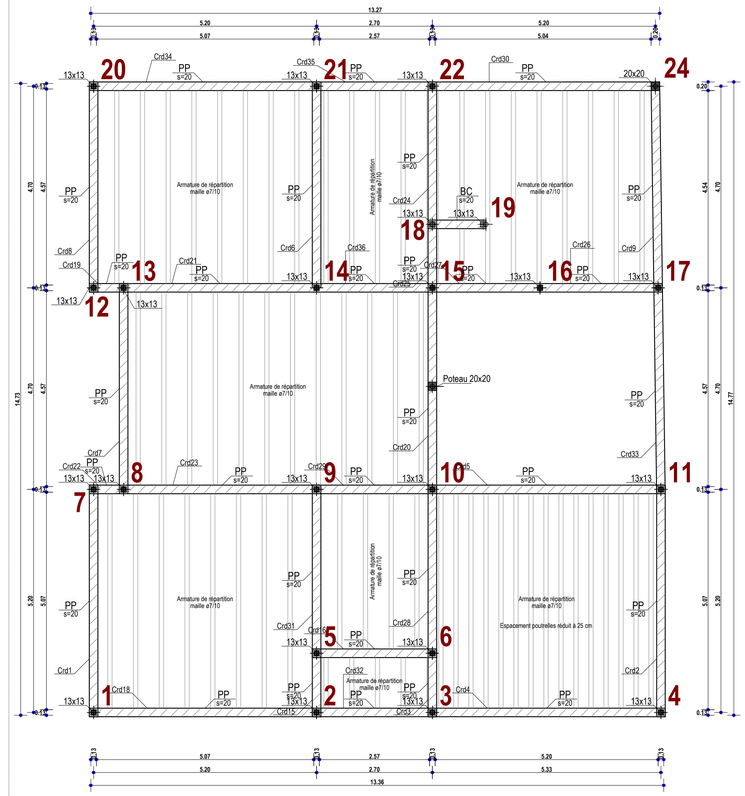

CHAINAGE

Id	Mtr	Htr	Base	Lngr	Arm long	Cadres
Crd18	Btn C25/30_B500B	0.13	0.20	5.40	4ø10	ø6/15
Crd19	Btn C25/30_B500B	0.13	0.20	1.58	4ø10	ø6/15
Crd16	Btn C25/30_B500B	0.13	0.20	2.90	4ø10	ø6/15
Crd3	Btn C25/30_B500B	0.13	0.20	1.58	4ø10	ø6/15
Crd4	Btn C25/30_B500B	0.13	0.20	5.53	4ø10	ø6/15
Crd1	Btn C25/30_B500B	0.13	0.20	5.40	4ø10	ø6/15
Crd2	Btn C25/30_B500B	0.13	0.20	5.40	4ø10	ø6/15
Crd5	Btn C25/30_B500B	0.13	0.20	5.53	4ø10	ø6/15
Crd8	Btn C25/30_B500B	0.13	0.20	4.90	4ø10	ø6/15
Crd9	Btn C25/30_B500B	0.13	0.20	4.80	4ø10	ø6/15
Crd6	Btn C25/30_B500B	0.13	0.20	4.80	4ø10	ø6/15
Crd7	Btn C25/30_B500B	0.13	0.20	4.90	4ø10	ø6/15
Crd30	Btn C25/30_B500B	0.13	0.20	5.30	4ø10	ø6/15
Crd31	Btn C25/30_B500B	0.13	0.20	4.02	4ø10	ø6/15
Crd28	Btn C25/30_B500B	0.13	0.20	3.92	4ø10	ø6/15
Crd29	Btn C25/30_B500B	0.13	0.20	2.90	4ø10	ø6/15
Crd32	Btn C25/30_B500B	0.13	0.20	2.90	4ø10	ø6/15
Crd25	Btn C25/30_B500B	0.13	0.20	2.70	4ø10	ø6/15
Crd26	Btn C25/30_B500B	0.13	0.20	2.70	4ø10	ø6/15
Crd33	Btn C25/30_B500B	0.13	0.20	4.80	4ø10	ø6/15
Crd34	Btn C25/30_B500B	0.13	0.20	5.30	4ø10	ø6/15
Crd21	Btn C25/30_B500B	0.13	0.20	4.50	4ø10	ø6/15
Crd22	Btn C25/30_B500B	0.13	0.20	0.80	4ø10	ø6/15
Crd23	Btn C25/30_B500B	0.13	0.20	3.80	4ø10	ø6/15
Crd20	Btn C25/30_B500B	0.13	0.20	4.60	4ø10	ø6/15
Crd24	Btn C25/30_B500B	0.13	0.20	4.60	4ø10	ø6/15
Crd27	Btn C25/30_B500B	0.13	0.20	2.85	4ø10	ø6/15
Crd35	Btn C25/30_B500B	0.13	0.20	2.51	4ø10	ø6/15
Crd36	Btn C25/30_B500B	0.13	0.20	3.32	4ø10	ø6/15
Crd5	Btn C25/30_B500B	0.13	0.20	1.48	4ø10	ø6/15

Id: Identifiant chaînage
Mtr: matériau
Htr: hauteur (en m)
Base: base (en m)
Lngr: longueur (en m)
Arm long: armatures longitudinales (nombre/diamètre en mm)
Cadres: armatures des cadres (diamètre en mm/espacement en cm)