Planta R/C — Moradia Martins Fixture

Fixture sintética bet_agent — ZERO PII — página 1

TOTAL = 7.50 (declarado)

3.00	4.00

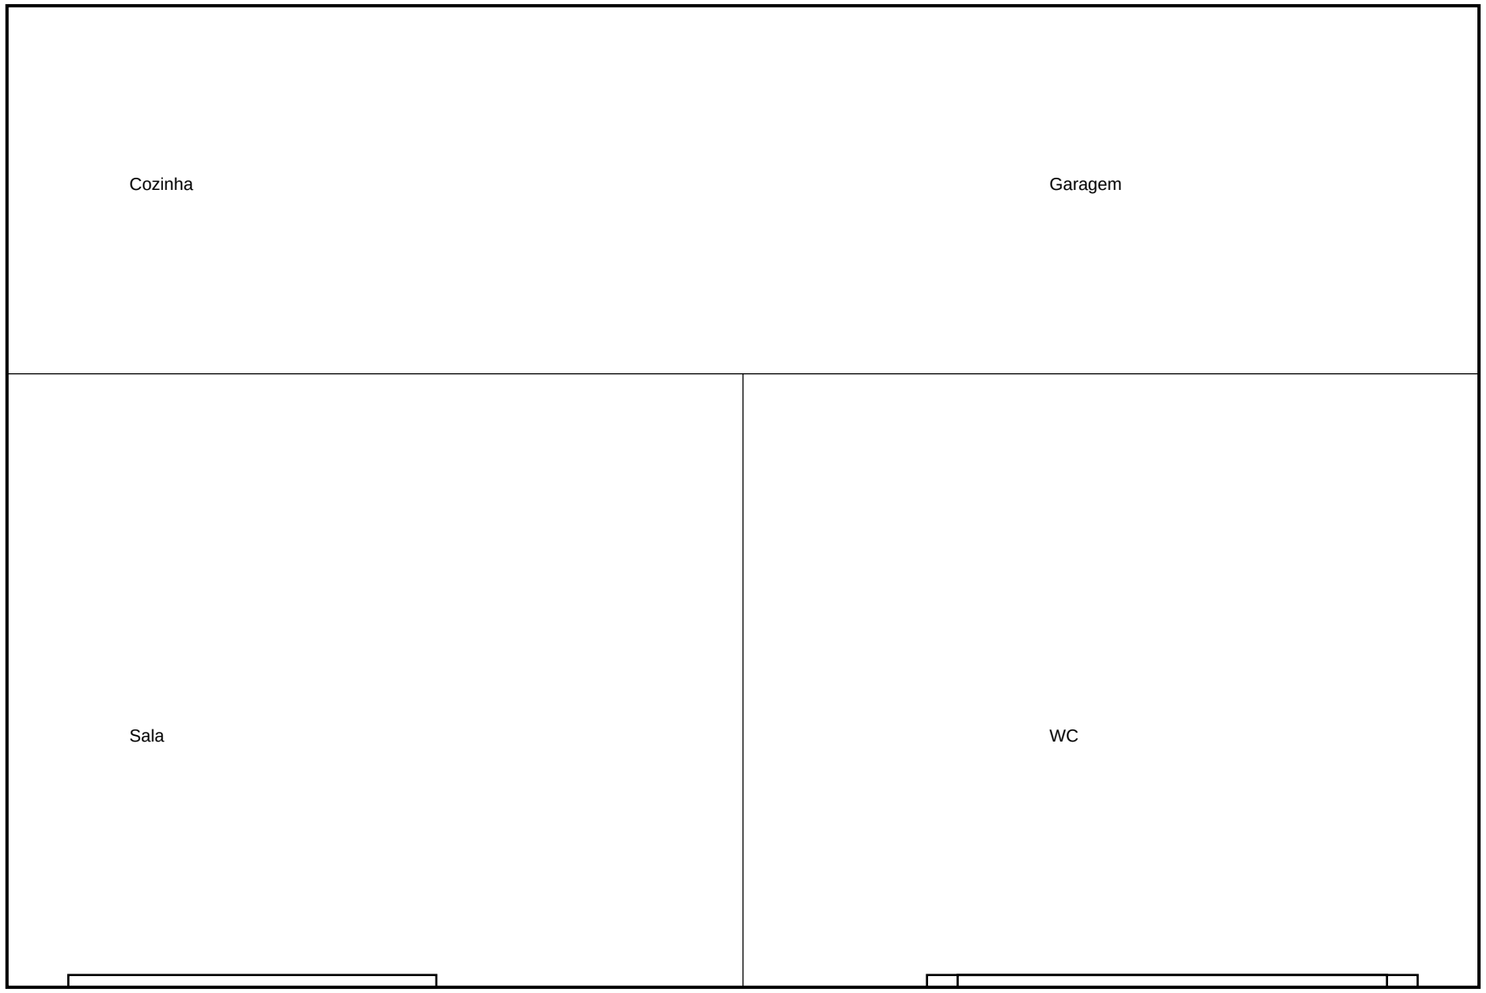

Fixture gerada para testes — não constitui projecto real.

Planta Cave — Moradia Martins Fixture

Fixture sintética bet_agent — ZERO PII — página 2

 

Fixture gerada para testes — não constitui projecto real.

Planta Sotao — Moradia Martins Fixture

Fixture sintética bet_agent — ZERO PII — página 3

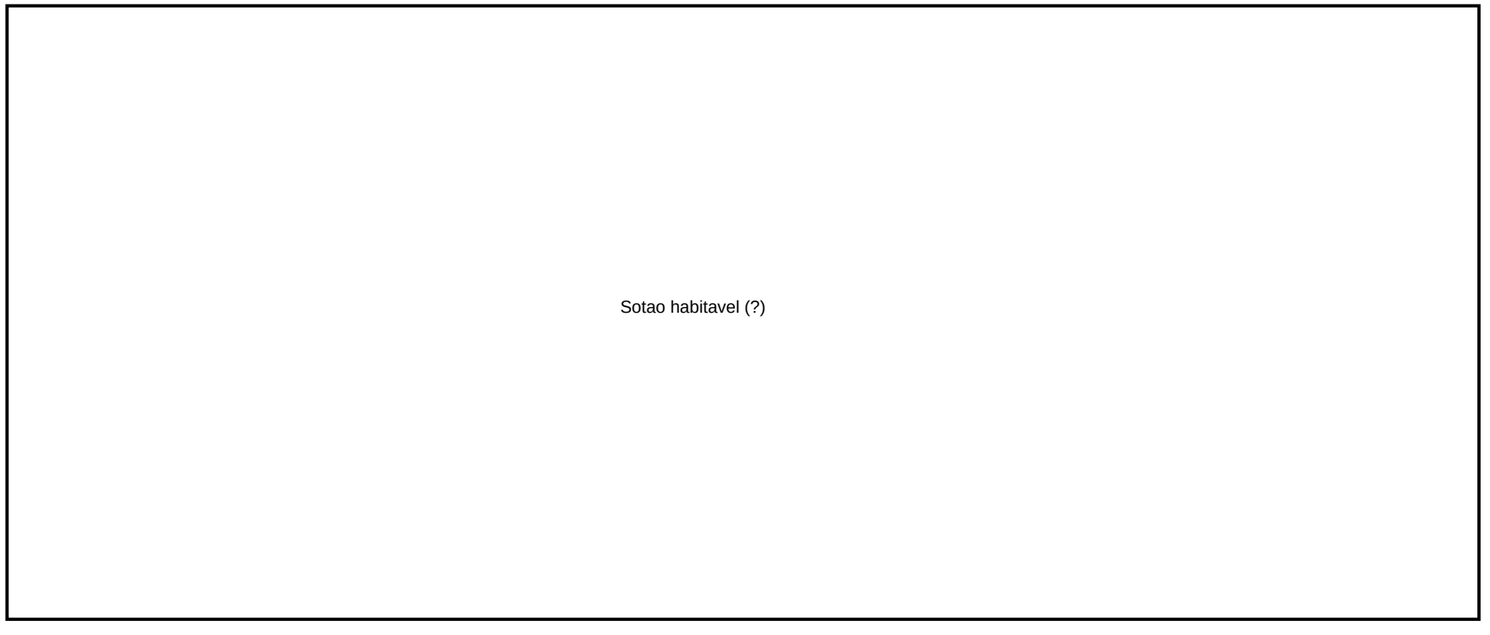

Altura livre: 1.70 a 2.20 m (variavel) - A CONFIRMAR em corte

Corte AA — Escada Moradia Martins Fixture

Fixture sintética bet_agent — ZERO PII — página 4

Pé-direito 1º andar = 2.70 m

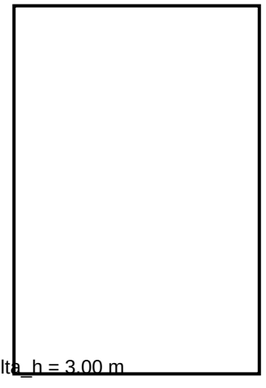

Escada: abertura disponivel = 1.20 m, delta_h = 3.00 m

Pé-direito R/C = 2.70 m

Quadro de areas — Moradia Martins Fixture

Fixture sintética bet_agent — ZERO PII — página 5

Compartimento	Area (m2)
Sala	25.00
Cozinha	15.00
WC	4.50
Garagem	30.00
Quarto 1	14.00
Quarto 2	12.00
Sotao	40.00