Planta de localização (ortofotomapa)



Legenda

- Limite do terreno
- Construção proposta


Fonte:
· Limite: indicada pelo requerente

Desenho esquemático gerado pelo ConstruPilot — a verificar, cotar e assinar por técnico habilitado antes da submissão.
Limite do terreno a confirmar por levantamento topográfico e certidão predial.

Processo	Moradia T4 — Rua do Monte 7, Padim da Graça, 4700-651 Braga
Requerente	—
Local	Padim da Graça, Braga, Portugal, Braga
Peça	Planta de localização (ortofotomapa)
Escala	sem escala — desenho esquemático
Data / folha	08/11/2026 · 1/16
Técnico autor	_____ (n.º de inscrição na Ordem)

Desenho esquemático gerado pelo ConstruPilot — a verificar, cotar e assinar por técnico habilitado antes da submissão.

Planta de implantação (esquemática)

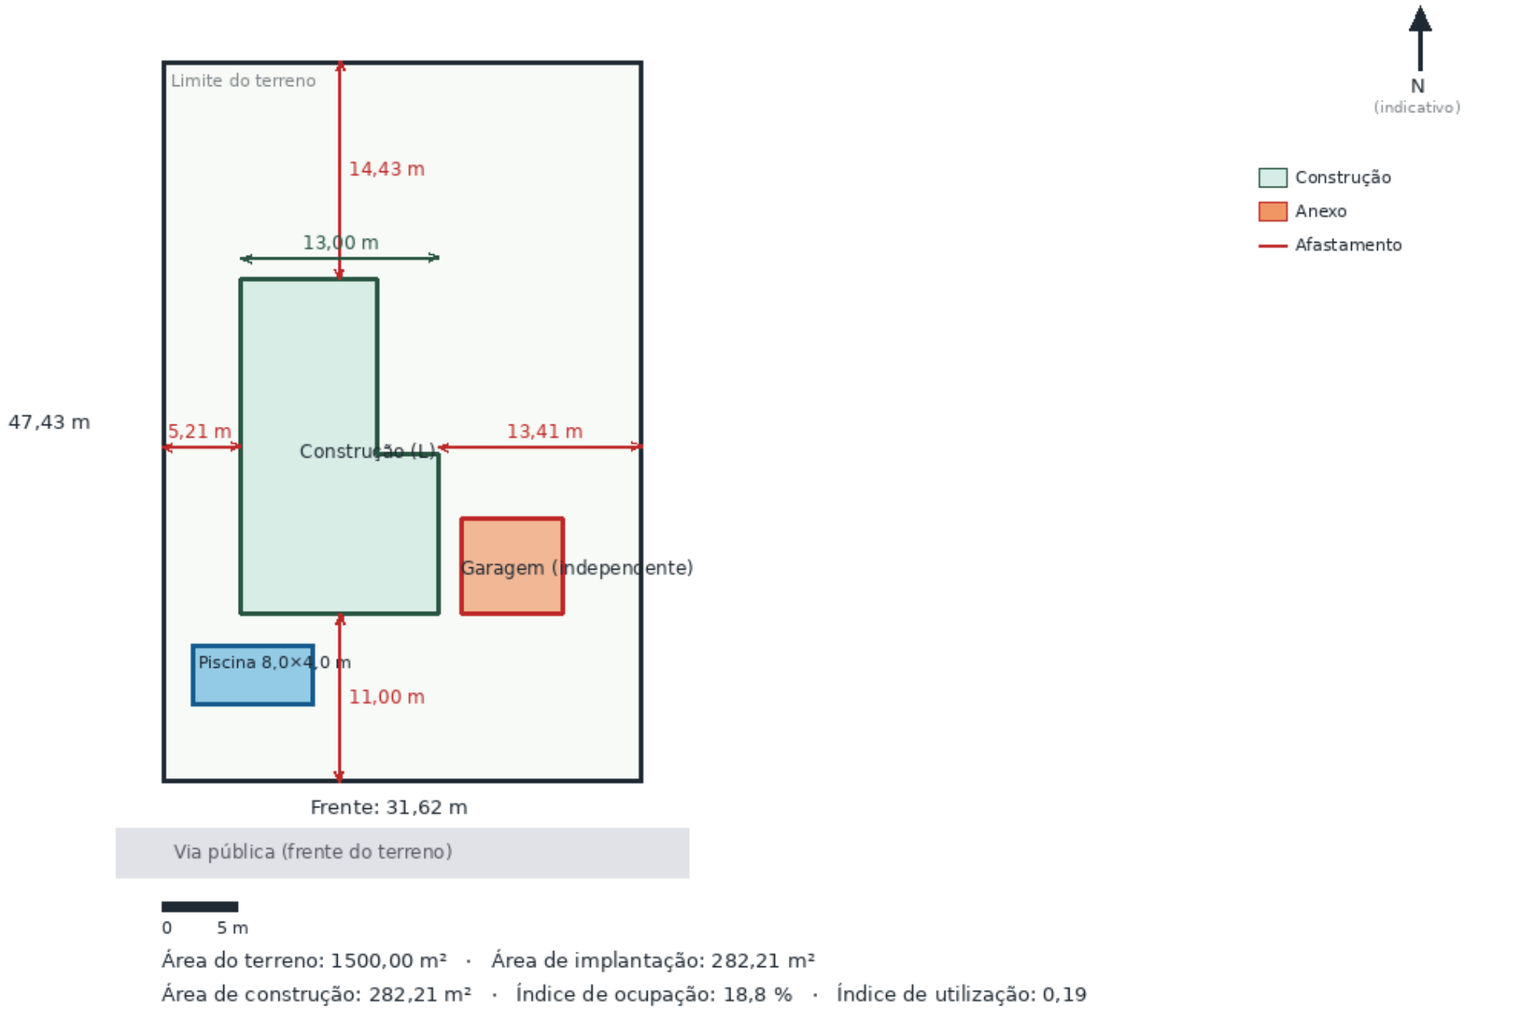


Área do terreno: 1500,00 m² · Área de implantação: 282,21 m²
Área de construção: 282,21 m² · Índice de ocupação: 18,8 % · Índice de utilização: 0,19

Desenho esquemático gerado pelo ConstruPilot — a verificar, cotar e assinar por técnico habilitado antes da submissão.
Terreno representado como retângulo — a substituir pelo levantamento topográfico.

Processo	Moradia T4 — Rua do Monte 7, Padim da Graça, 4700-651 Braga
Requerente	—
Local	Padim da Graça, Braga, Portugal, Braga
Peça	Planta de implantação
Escala	sem escala — desenho esquemático
Data / folha	08/11/2026 · 2/16
Técnico autor	_____ (n.º de inscrição na Ordem)

Desenho esquemático gerado pelo ConstruPilot — a verificar, cotar e assinar por técnico habilitado antes da submissão.

Vista axonométrica do volume (esquemática)

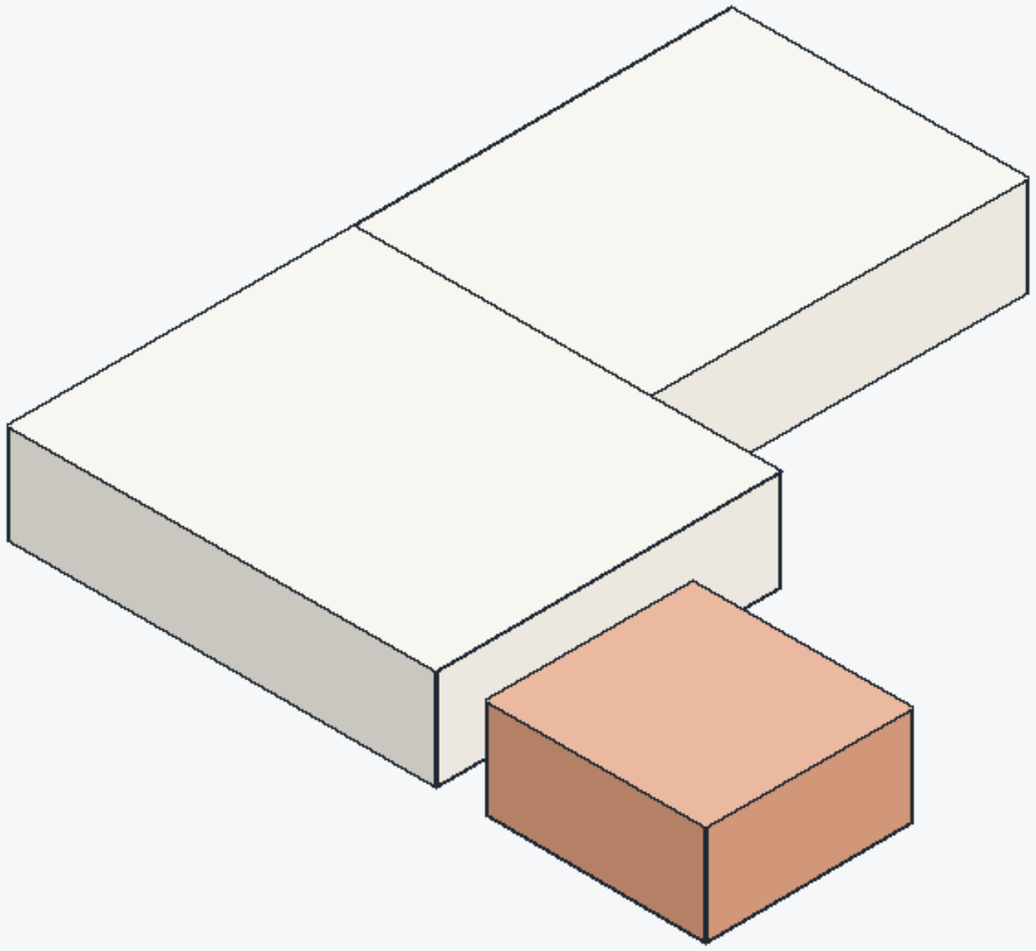

Vista a partir da frente (via pública) e do lado direito.

Altura total ≈ 3,50 m · 1 piso(s) · área de implantação 282,21 m²

Desenho esquemático gerado pelo ConstruPilot — a verificar, cotar e assinar por técnico habilitado antes da submissão.

Processo	Moradia T4 — Rua do Monte 7, Padim da Graça, 4700-651 Braga
Requerente	—
Local	Padim da Graça, Braga, Portugal, Braga
Peça	Vista axonométrica
Escala	sem escala — desenho esquemático
Data / folha	08/11/2026 · 3/16
Técnico autor	_____ (n.º de inscrição na Ordem)

Desenho esquemático gerado pelo ConstruPilot — a verificar, cotar e assinar por técnico habilitado antes da submissão.


Planta do rés-do-chão — arquitetura

Escala 1:100 (folha A3)

Parede exterior 0,30 m (alvenaria + isolamento + revestimento)

Parede interior 0,12 m

Área útil total do piso: 225,96 m² · pé-direito livre 2,70 m

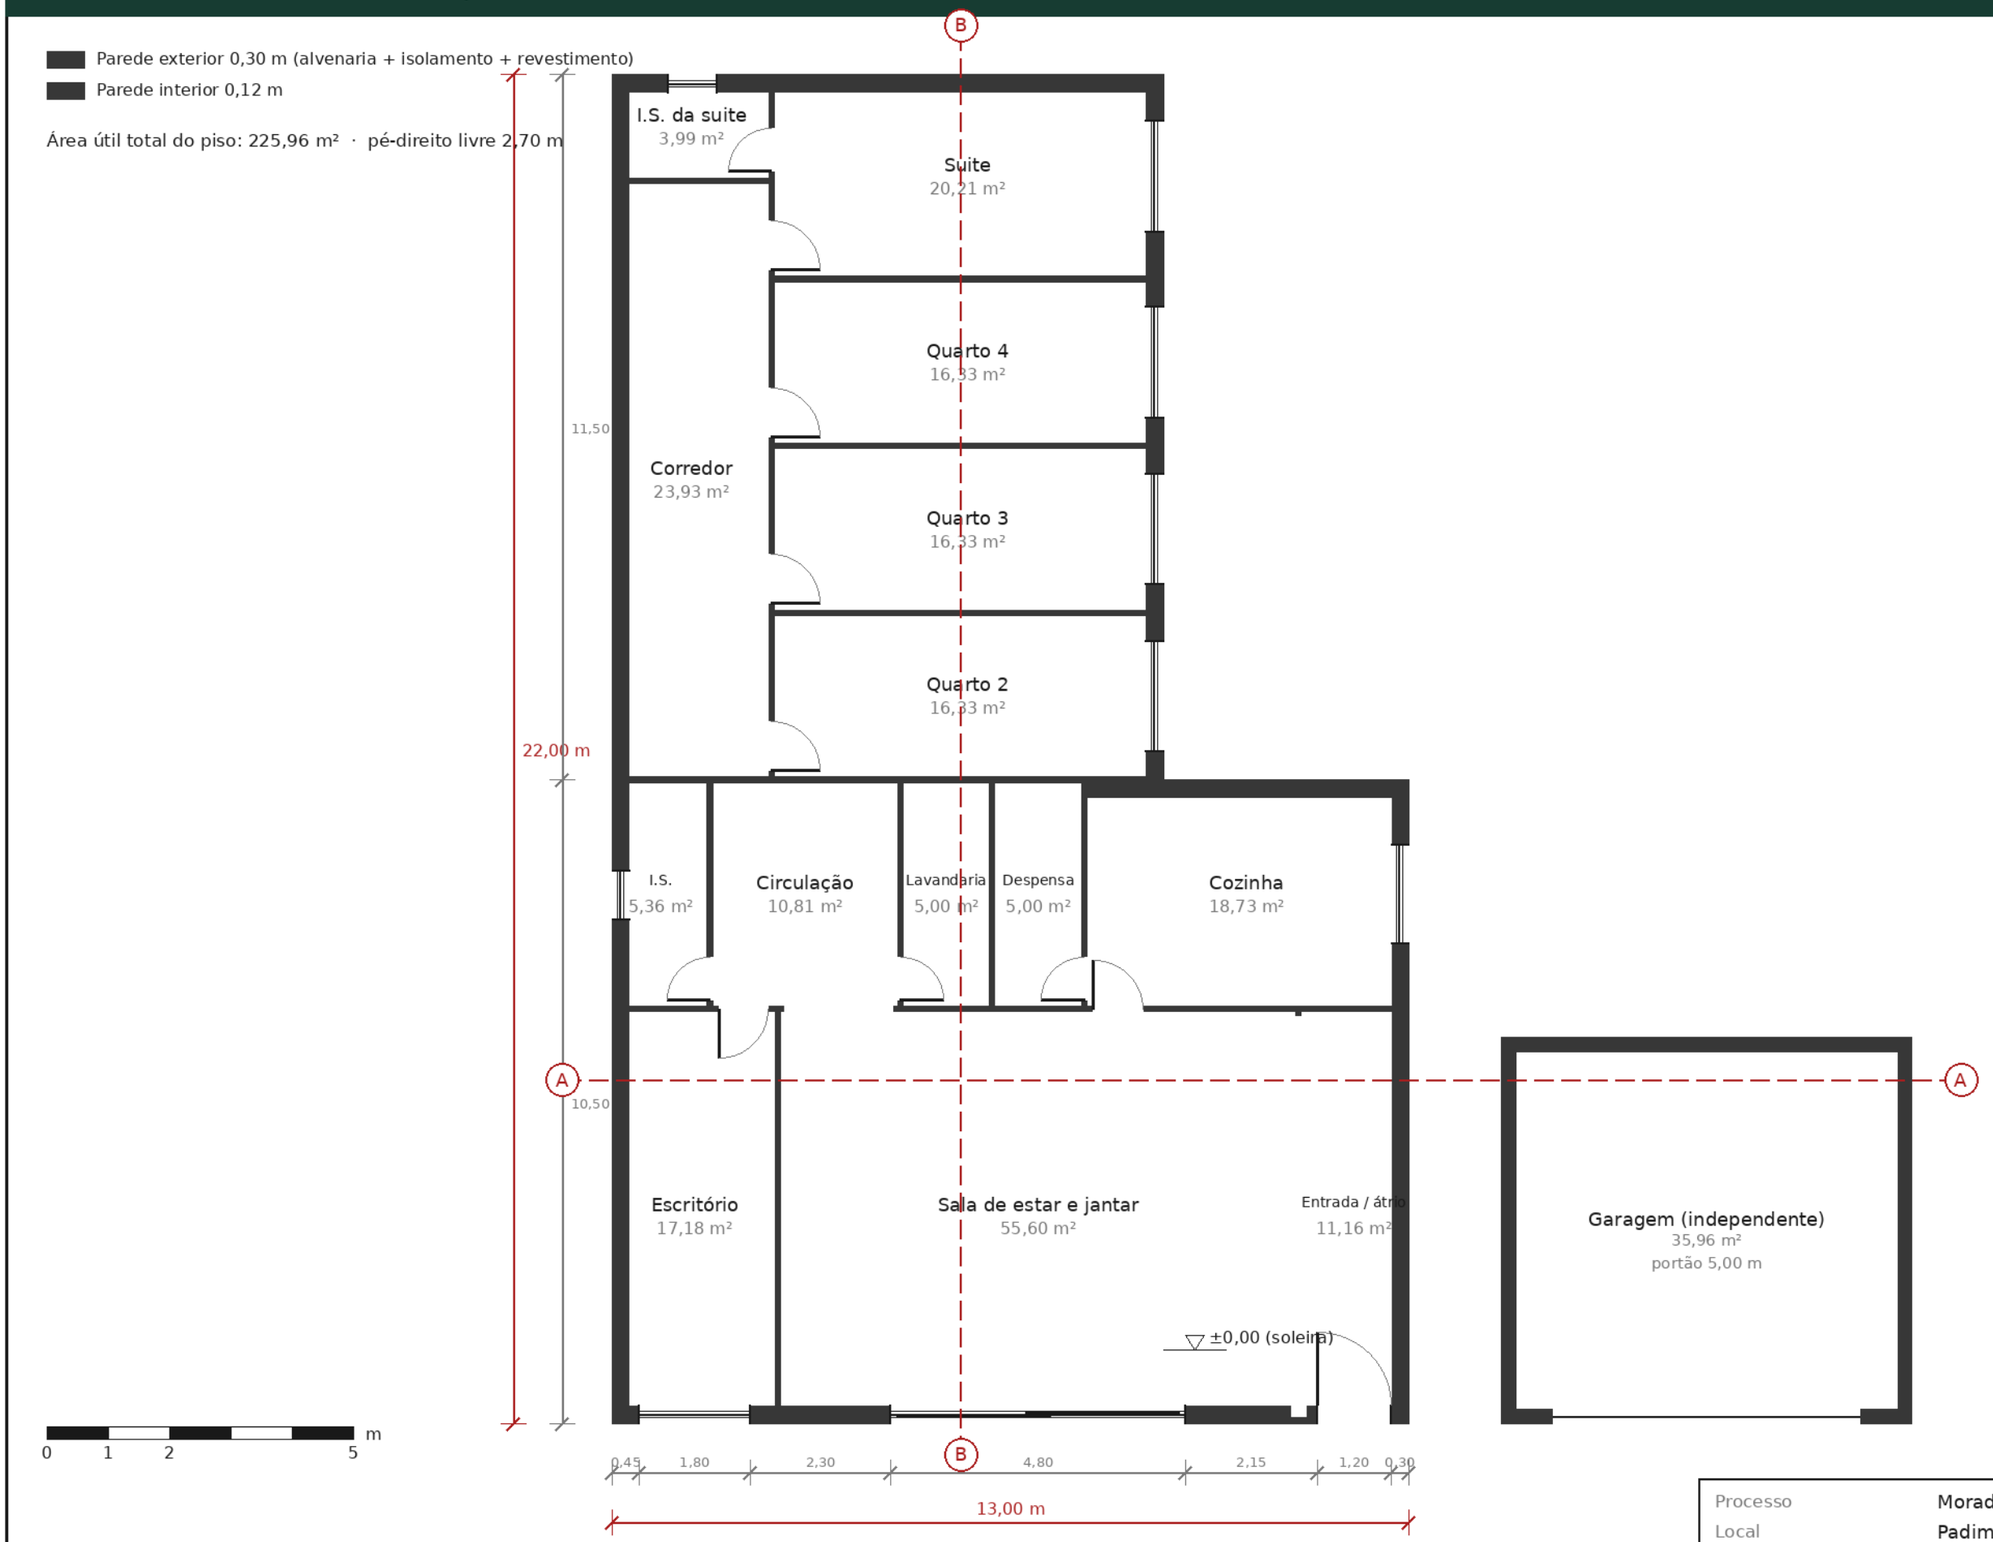


Processo	Moradia T4 — Rua do Monte 7, Padim da Graça, 4700-
Local	Padim da Graça, Braga, Portugal · Braga
Requerente	a completar
Peça	Planta do rés-do-chão
Escala	1:100
Data	08/11/2026
Autor do projeto	_____ n.º OA _____

Peça desenhada gerada pelo ConstruPilot a partir dos dados do processo — a verificar, completar e assinar por arquiteto inscrito na OA antes da submissão (art.º 10.º RJUE).

Planta de cobertura

Escala 1:100 (folha A3)

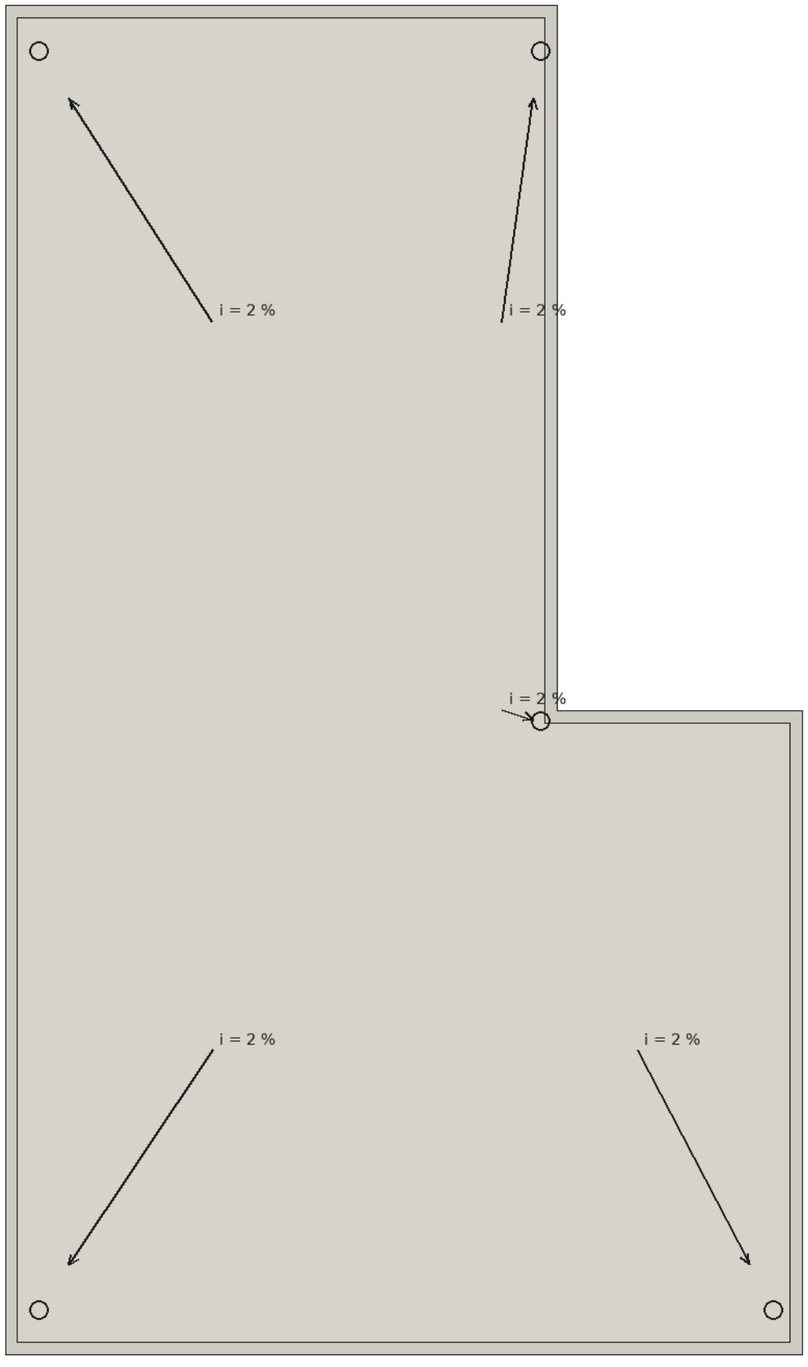

Garagem — cob. plana i = 2 %

Cobertura plana invertida, não acessível (exceto manutenção):
laje de betão armado + betonilha de forma (i ≥ 2 %) + impermeabilização + isolamento térmico XPS + geotêxtil + seixo rolado
Platibanda 0,20 m de espessura até à cota +3,50 m; rufo metálico de capeamento
Tubos de queda Ø 90 mm (indicados ◯) ligados à rede de águas pluviais


0 1 2 5 m

Processo	Moradia T4 — Rua do Monte 7, Padim da Graça, 4700-
Local	Padim da Graça, Braga, Portugal · Braga
Requerente	a completar
Peça	Planta de cobertura
Escala	1:100
Data	08/11/2026
Autor do projeto	_____ n.º OA _____


Peça desenhada gerada pelo ConstruPilot a partir dos dados do processo — a verificar, completar e assinar por arquiteto inscrito na OA antes da submissão (art.º 10.º RJUE).

Alçado principal e alçado de tardoz

Escala 1:100 (folha A3)

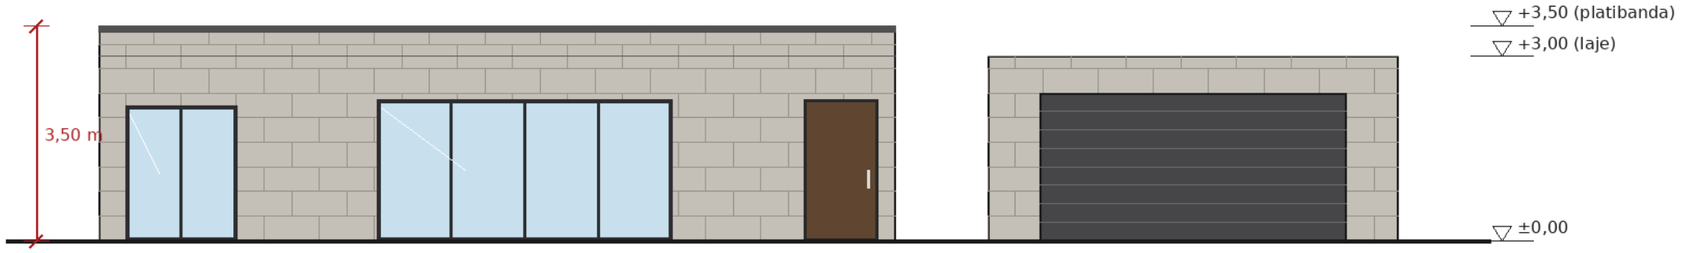

Alçado principal

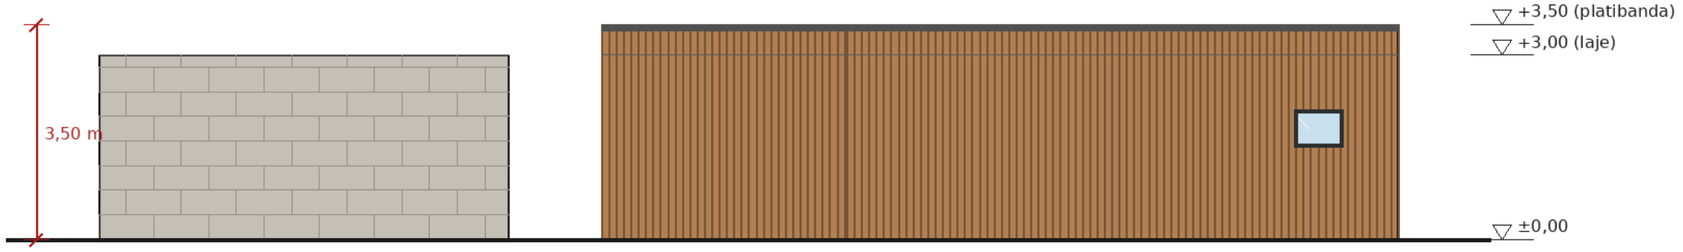

Alçado de tardoz

Revestimentos:

- granito natural bujardado
- ripado vertical de madeira

Caixilharia: aluminio antracite, vidro duplo


0 1 2 5 m

Processo	Moradia T4 — Rua do Monte 7, Padim da Graça, 4700-
Local	Padim da Graça, Braga, Portugal · Braga
Requerente	a completar
Peça	Alçado principal / Alçado de tardoz
Escala	1:100
Data	08/11/2026
Autor do projeto	_____ n.º OA _____

Peça desenhada gerada pelo ConstruPilot a partir dos dados do processo — a verificar, completar e assinar por arquiteto inscrito na OA antes da submissão (art.º 10.º RJUE).

Alçado lateral esquerdo e alçado lateral direito

Escala 1:100 (folha A3)

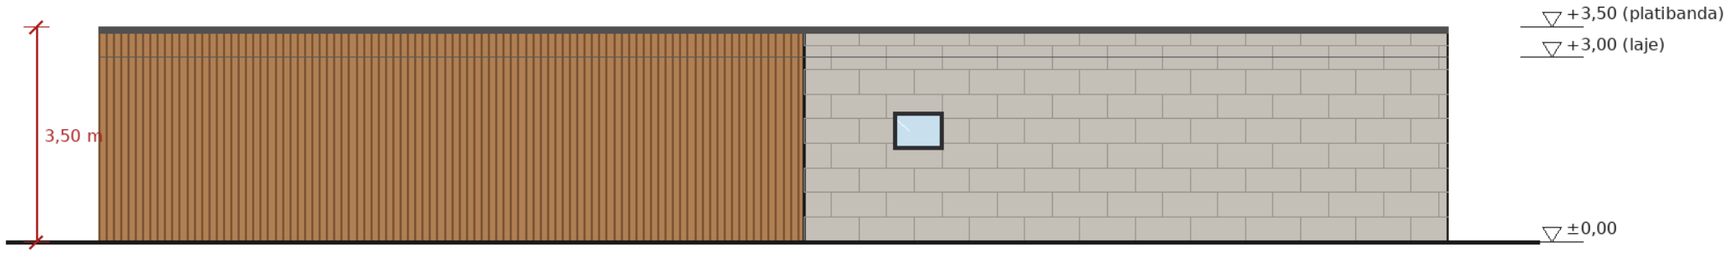

Alçado lateral esquerdo



Alçado lateral direito

Revestimentos:

- granito natural bujardado
- ripado vertical de madeira

Caixilharia: aluminio antracite, vidro duplo


0 1 2 5 m

Processo	Moradia T4 — Rua do Monte 7, Padim da Graça, 4700-
Local	Padim da Graça, Braga, Portugal · Braga
Requerente	a completar
Peça	Alçado lateral esquerdo / Alçado lateral direito
Escala	1:100
Data	08/11/2026
Autor do projeto	_____ n.º OA _____


Peça desenhada gerada pelo ConstruPilot a partir dos dados do processo — a verificar, completar e assinar por arquiteto inscrito na OA antes da submissão (art.º 10.º RJUE).

Cortes A-A e B-B

Escala 1:100 (folha A3)

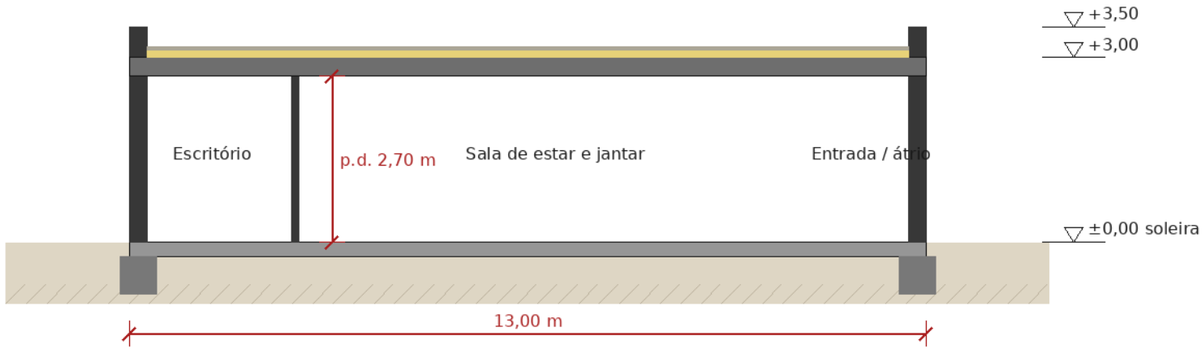

Corte A-A (transversal)

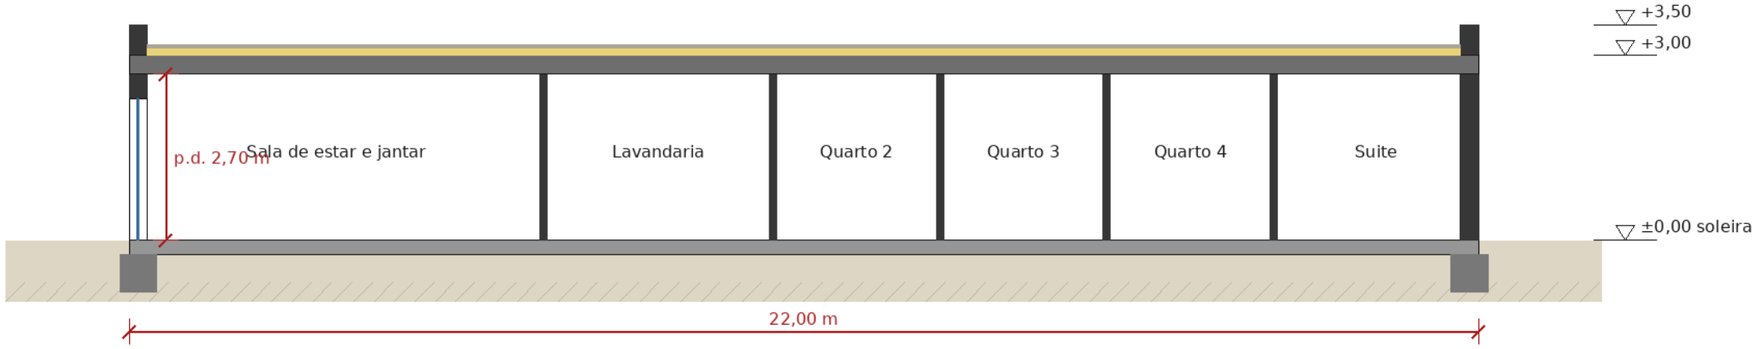

Corte B-B (longitudinal)

- Laje de cobertura em betão armado 0,30 m (incl. revestimentos)
- Isolamento térmico XPS + seixo
- Paredes exteriores 0,30 m · interiores 0,12 m
- Laje térrea sobre caixa de brita e isolamento
- Fundações diretas (sapatas) — a dimensionar no projeto de estabilidade

0 1 2 5 m


Processo	Moradia T4 — Rua do Monte 7, Padim da Graça, 4700-
Local	Padim da Graça, Braga, Portugal · Braga
Requerente	a completar
Peça	Cortes transversal A-A e longitudinal B-B
Escala	1:100
Data	08/11/2026
Autor do projeto	_____ n.º OA _____

Peça desenhada gerada pelo ConstruPilot a partir dos dados do processo — a verificar, completar e assinar por arquiteto inscrito na OA antes da submissão (art.º 10.º RJUE).


Piscina — planta e corte

Escala 1:50 (folha A3)

Cais / lajeado em granito antiderrapante, 1,20 m de largura

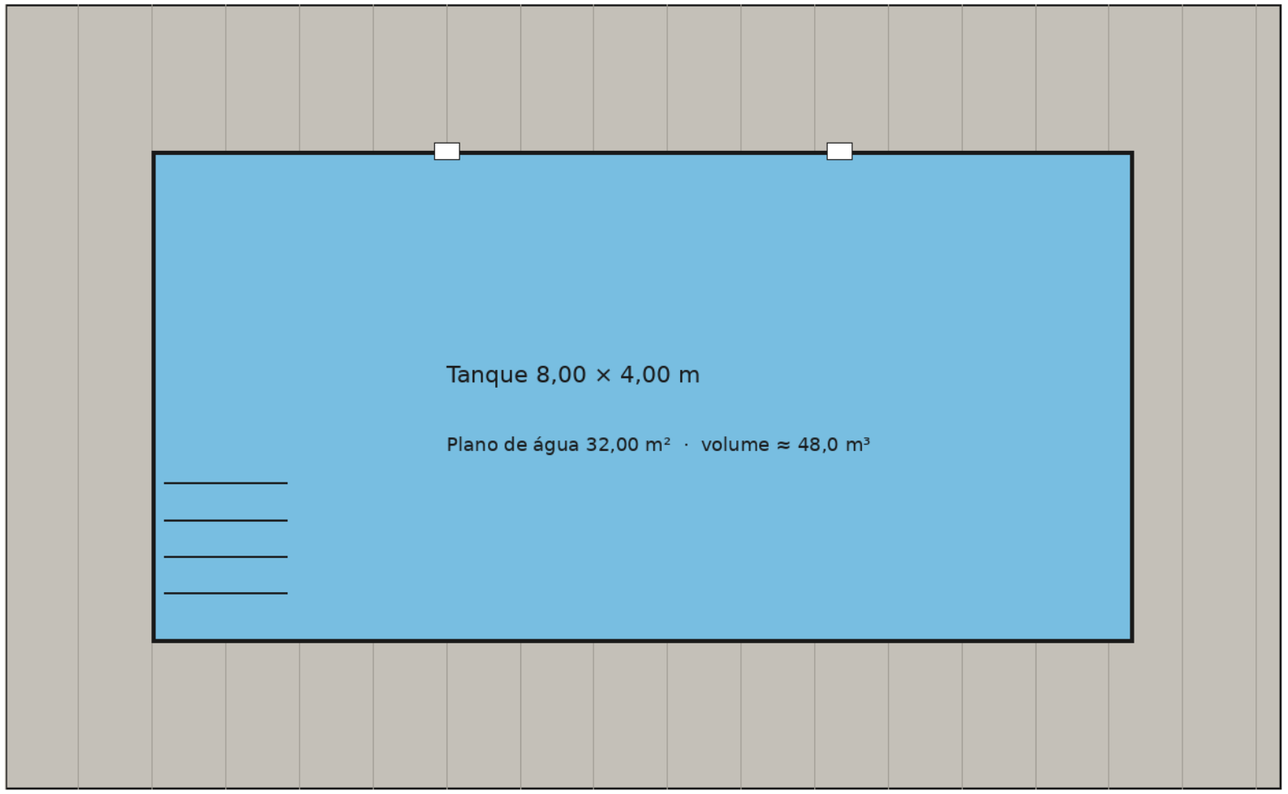

- Implantação (coordenadas do terreno): x = 2,00 m, y = 5,00 m
- Distância à fachada principal da casa: 2,00 m
- Distância ao limite frontal: 5,00 m · ao limite lateral: 2,00 m
- Piscina descoberta, sem cobertura — não conta para a área de implantação
- Casa das máquinas enterrada junto ao tanque (filtração + bomba de calor)
- Vedação ou cobertura de segurança recomendada (segurança de crianças)
- Descarga para a rede pluvial / vala, conforme parecer municipal

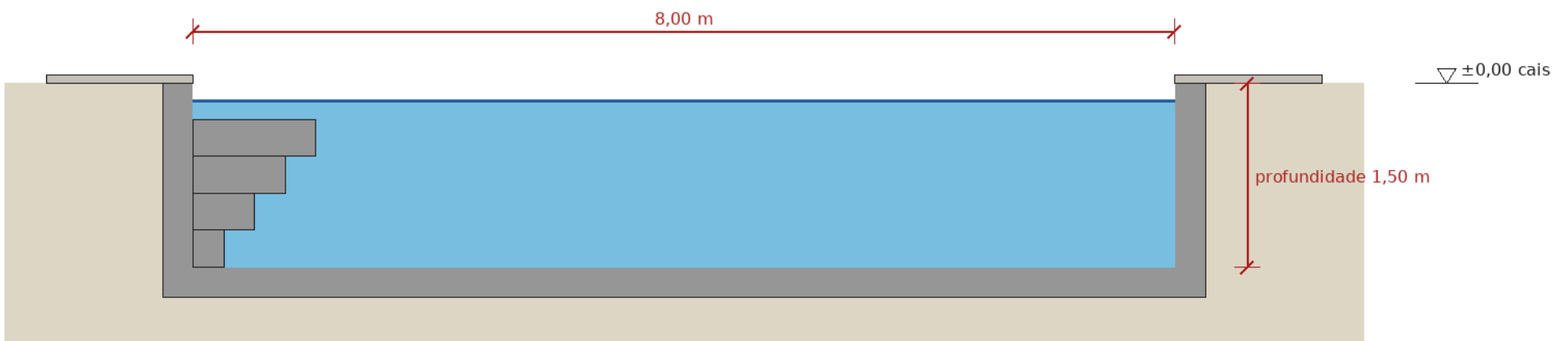

Corte longitudinal — tanque em betão armado 0,25 m, impermeabilizado e revestido




Processo	Moradia T4 — Rua do Monte 7, Padim da Graça, 4700-
Local	Padim da Graça, Braga, Portugal · Braga
Requerente	a completar
Peça	Piscina: planta e corte longitudinal
Escala	1:50
Data	08/11/2026
Autor do projeto	_____ n.º OA _____

Peça desenhada gerada pelo ConstruPilot a partir dos dados do processo — a verificar, completar e assinar por arquiteto inscrito na OA antes da submissão (art.º 10.º RJUE).

0 10 m

Implantação — arranjos exteriores e vegetação ilustrativos; medidas nas peças desenhadas.

N

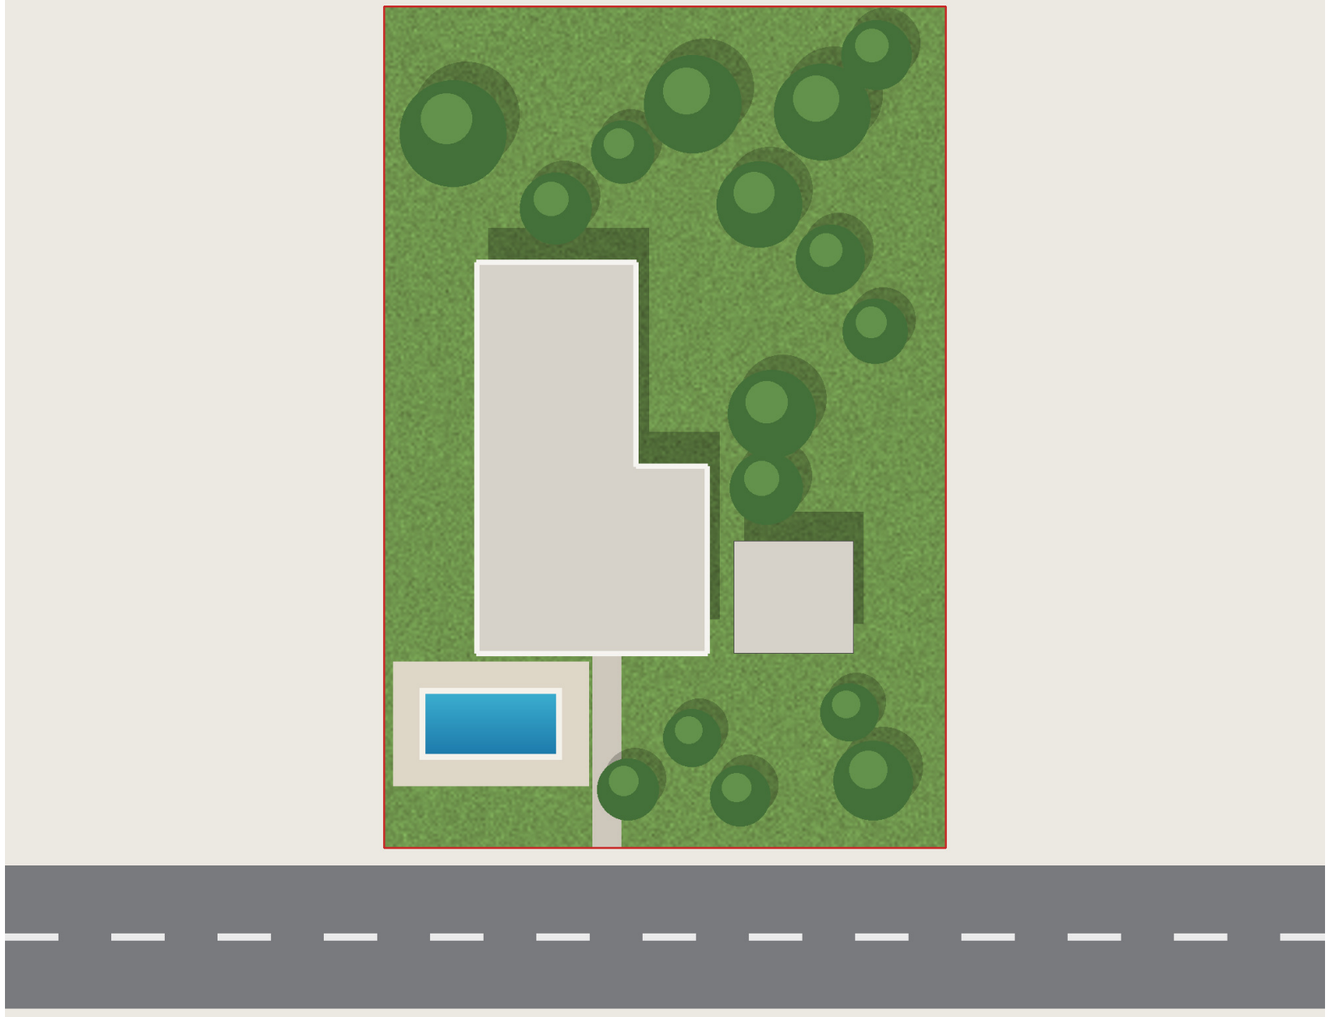

Processo	Moradia T4 — Rua do Monte 7, Padim da Graça, 4700-651 Braga
Requerente	—
Local	Padim da Graça, Braga, Portugal, Braga
Peça	Planta de implantação a cores (à escala)
Escala	sem escala — desenho esquemático
Data / folha	08/11/2026 · 10/16
Técnico autor	_____ (n.º de inscrição na Ordem)

Desenho esquemático gerado pelo ConstruPilot — a verificar, cotar e assinar por técnico habilitado antes da submissão.



Processo	Moradia T4 — Rua do Monte 7, Padim da Graça, 4700-651 Braga
Requerente	—
Local	Padim da Graça, Braga, Portugal, Braga
Peça	Simulação fotorrealista — perspetiva (geometria verificada com o proje
Escala	sem escala — desenho esquemático
Data / folha	08/11/2026 · 11/16
Técnico autor	_____ (n.º de inscrição na Ordem)

Desenho esquemático gerado pelo ConstruPilot — a verificar, cotar e assinar por técnico habilitado antes da submissão.



Processo	Moradia T4 — Rua do Monte 7, Padim da Graça, 4700-651 Braga
Requerente	—
Local	Padim da Graça, Braga, Portugal, Braga
Peça	Simulação fotorrealista — vista da piscina (ilustrativa, aprovada pelo
Escala	sem escala — desenho esquemático
Data / folha	08/11/2026 · 12/16
Técnico autor	_____ (n.º de inscrição na Ordem)

Desenho esquemático gerado pelo ConstruPilot — a verificar, cotar e assinar por técnico habilitado antes da submissão.



Processo	Moradia T4 — Rua do Monte 7, Padim da Graça, 4700-651 Braga
Requerente	—
Local	Padim da Graça, Braga, Portugal, Braga
Peça	Simulação fotorrealista — vista da frente (geometria verificada com o
Escala	sem escala — desenho esquemático
Data / folha	08/11/2026 · 13/16
Técnico autor	_____ (n.º de inscrição na Ordem)

Desenho esquemático gerado pelo ConstruPilot — a verificar, cotar e assinar por técnico habilitado antes da submissão.



Processo	Moradia T4 — Rua do Monte 7, Padim da Graça, 4700-651 Braga
Requerente	—
Local	Padim da Graça, Braga, Portugal, Braga
Peça	Simulação fotorrealista — vista do jardim (geometria verificada com o
Escala	sem escala — desenho esquemático
Data / folha	08/11/2026 · 14/16
Técnico autor	_____ (n.º de inscrição na Ordem)

Desenho esquemático gerado pelo ConstruPilot — a verificar, cotar e assinar por técnico habilitado antes da submissão.



Processo	Moradia T4 — Rua do Monte 7, Padim da Graça, 4700-651 Braga
Requerente	—
Local	Padim da Graça, Braga, Portugal, Braga
Peça	Simulação fotorrealista — vista aérea (geometria verificada com o proj
Escala	sem escala — desenho esquemático
Data / folha	08/11/2026 · 15/16
Técnico autor	_____ (n.º de inscrição na Ordem)

Desenho esquemático gerado pelo ConstruPilot — a verificar, cotar e assinar por técnico habilitado antes da submissão.



Processo	Moradia T4 — Rua do Monte 7, Padim da Graça, 4700-651 Braga
Requerente	—
Local	Padim da Graça, Braga, Portugal, Braga
Peça	Simulação fotorrealista — interior — cozinha (geometria verificada com
Escala	sem escala — desenho esquemático
Data / folha	08/11/2026 · 16/16
Técnico autor	_____ (n.º de inscrição na Ordem)

Desenho esquemático gerado pelo ConstruPilot — a verificar, cotar e assinar por técnico habilitado antes da submissão.