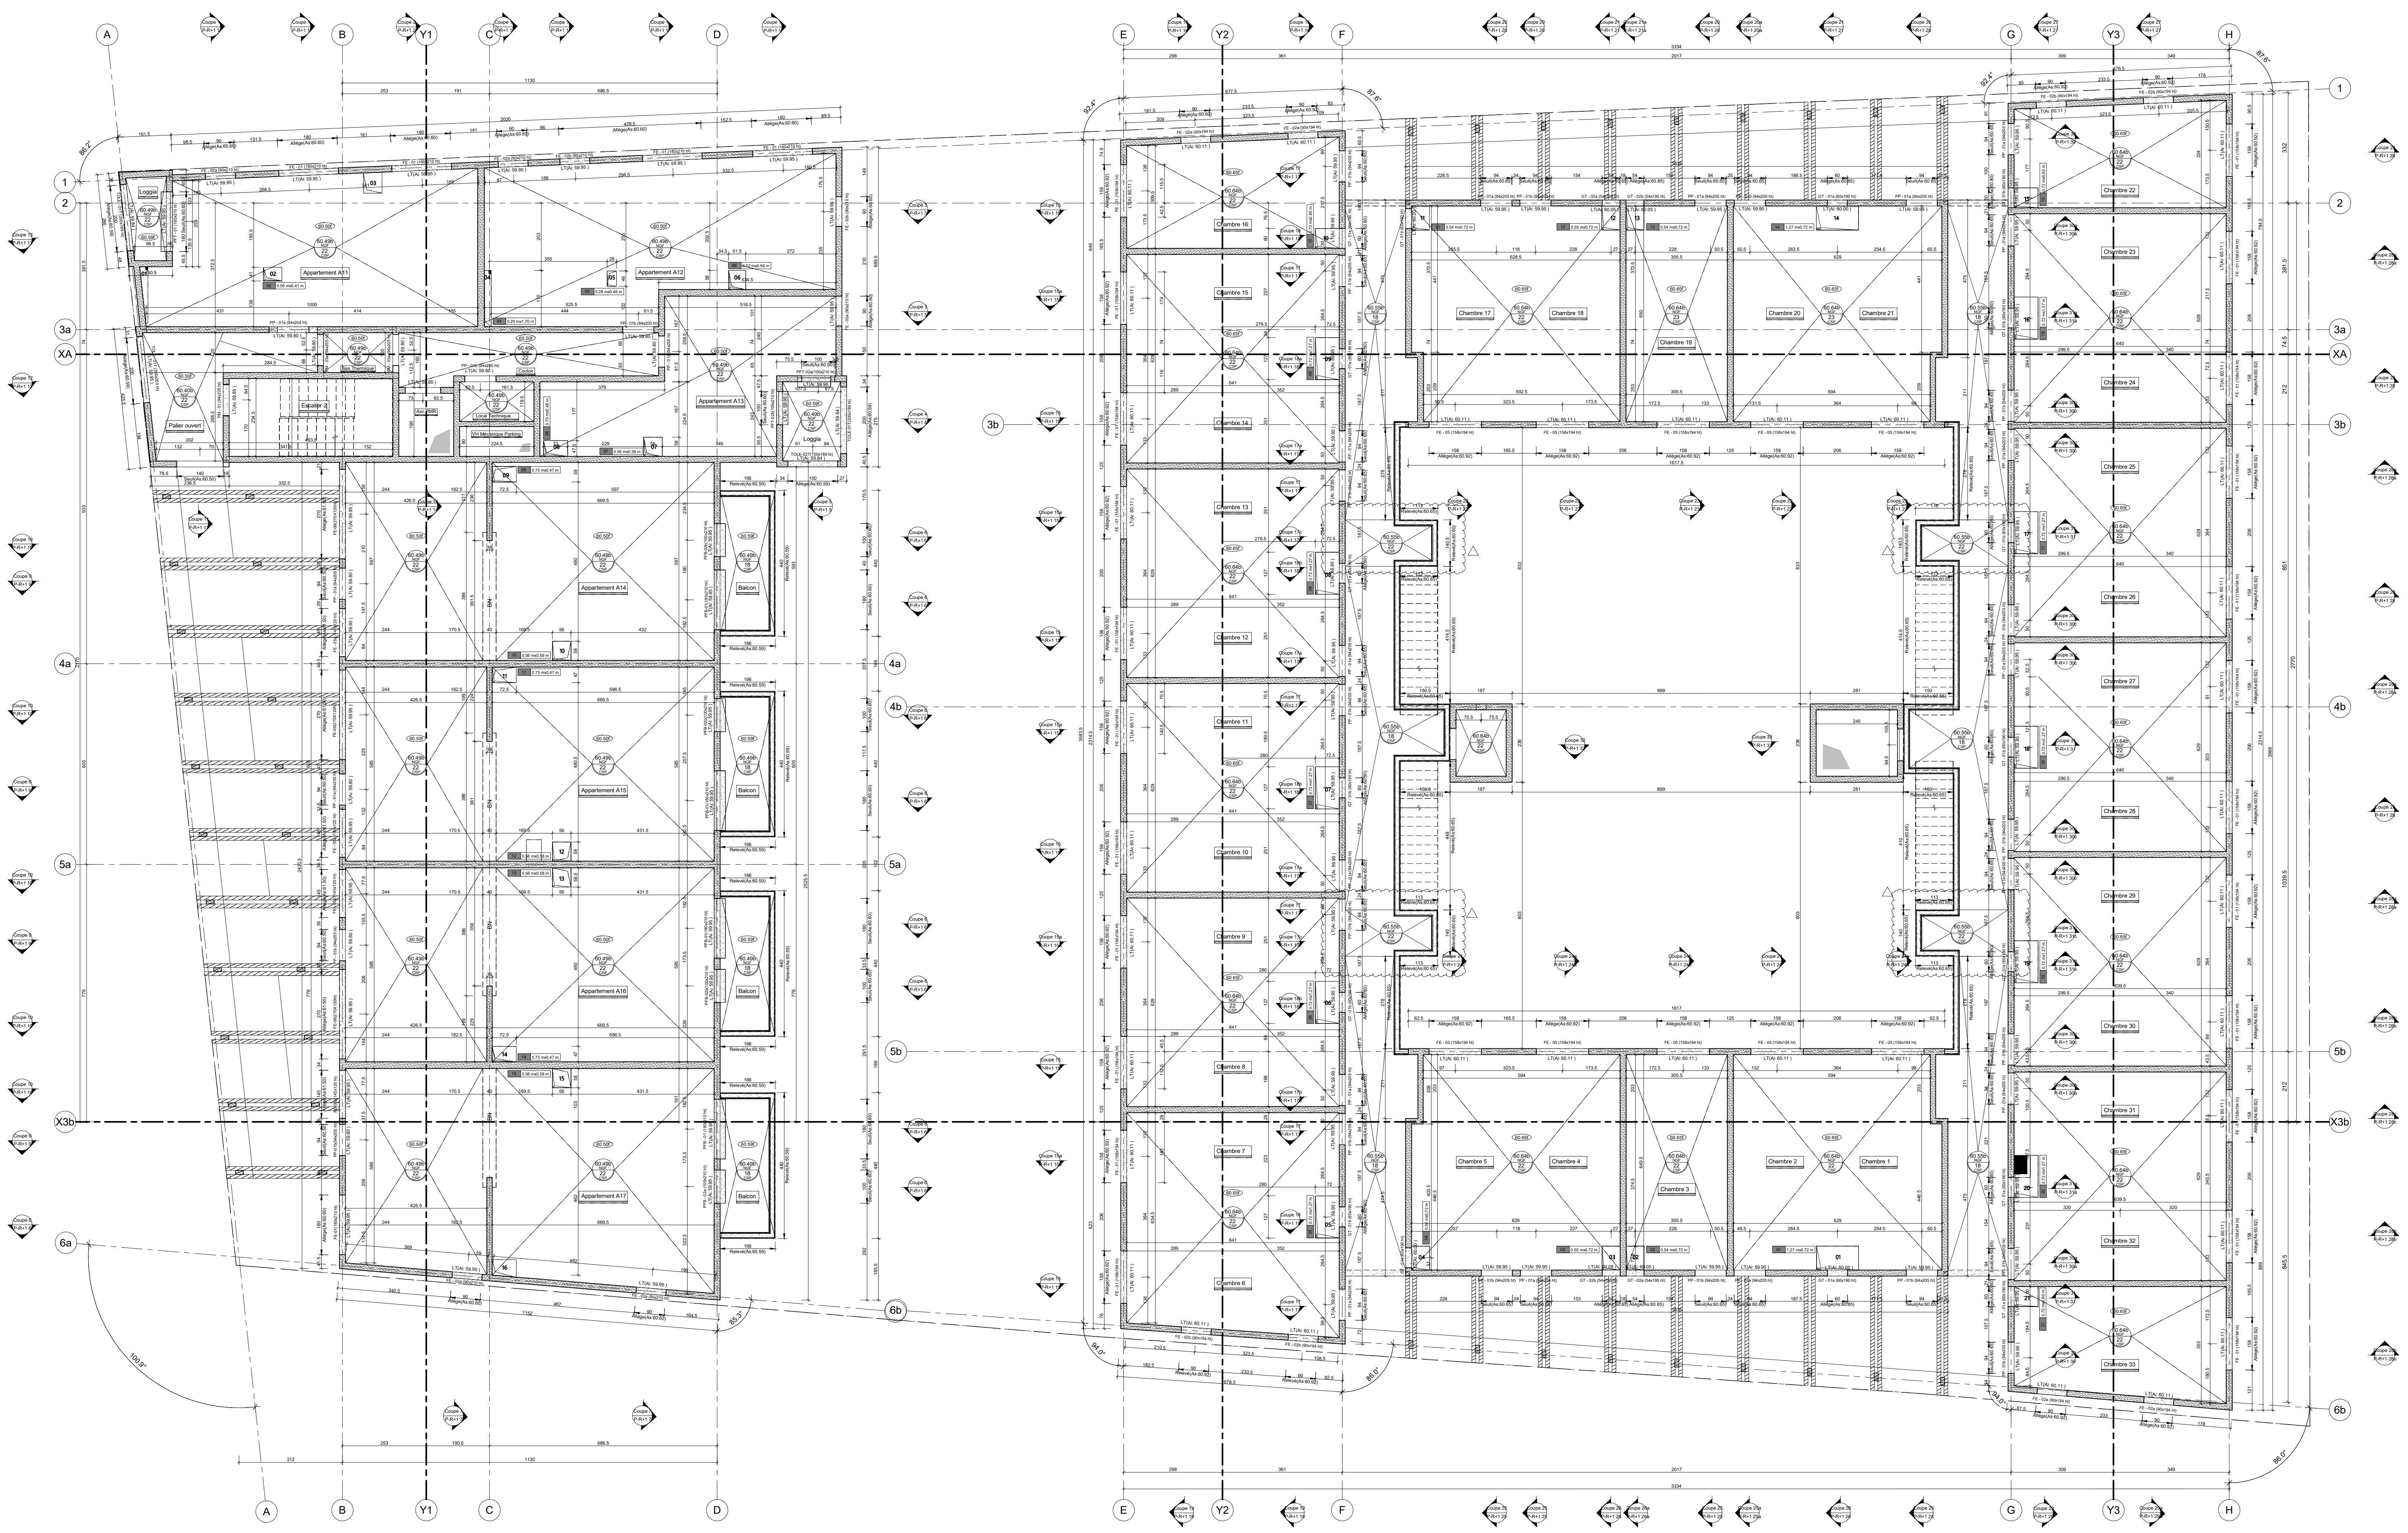

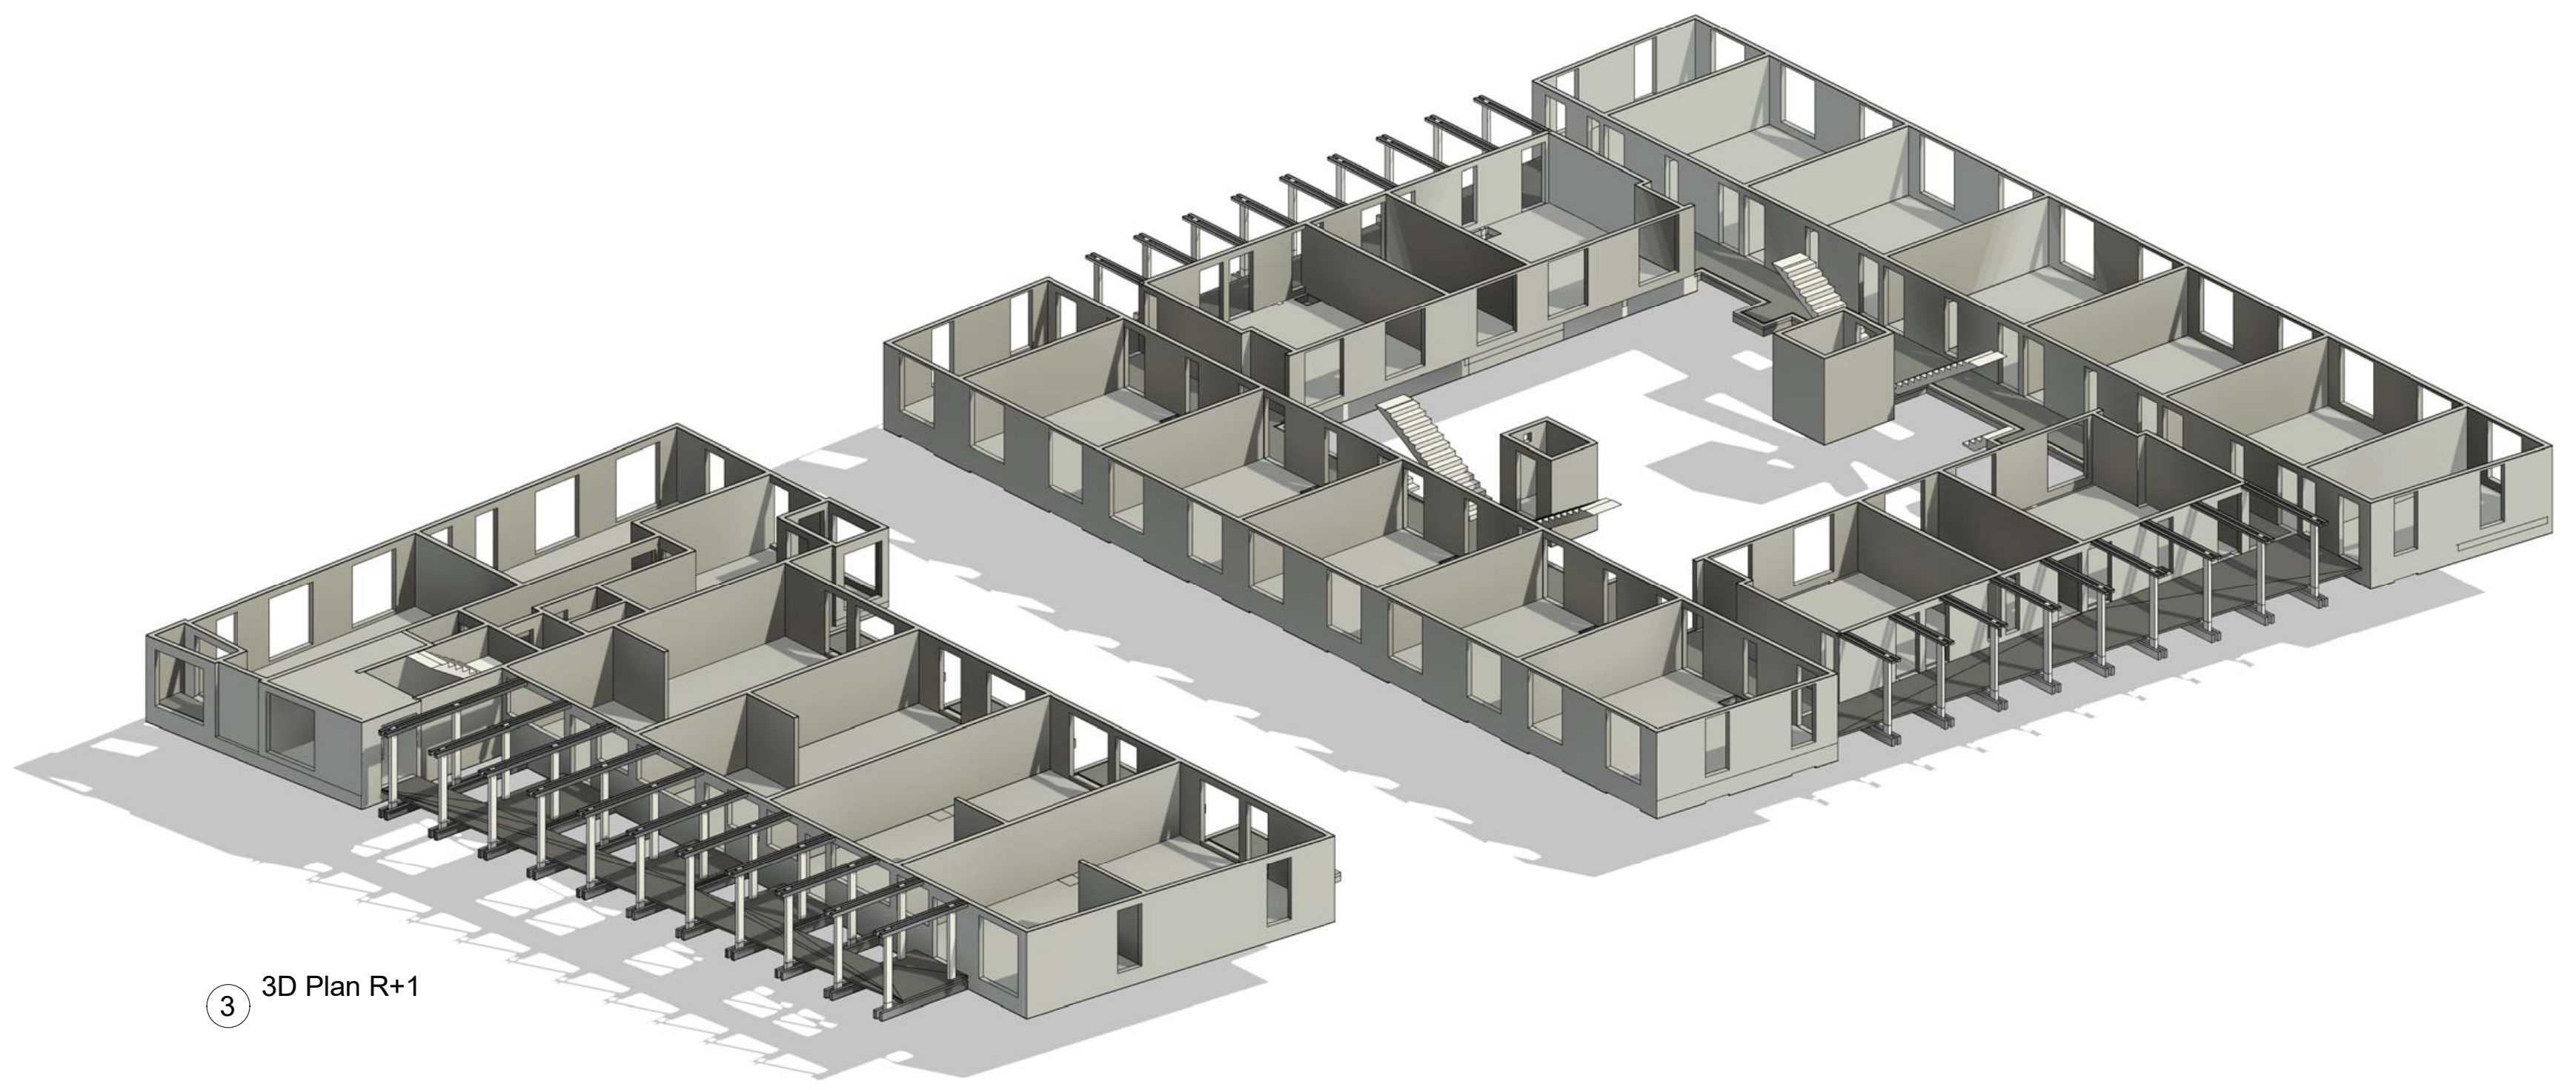

3 3D Plan R+1

HYPOTHESES DE CALCULS sauf indication contraire

CARACTÉRISTIQUES DU SOL:

- Remblais de profondeur 3.5m
- Marnes panachées de 1.5m de profondeur
- Le bâtiment sera fondé sur des fondations superficielles par semelles encastrées au minimum de 30cm dans les marnes panchées reconnues à partir de 3.5 ou 4.5m de profondeur.

NIVEAUX D'EAUX:

- EAUX HAUTES : 52 NGF

Pour les remontées de nappe d'importance supérieure à la décennale, le sous-sol est à considérer comme inondable. Le plancher bas sera équipé d'évents.

ACIERS:

- Acier HA: Fe E 500
- Acier dx: Fe E 235
- Treillis Soudés: Fe Te 500

CARACTÉRISTIQUE DU BÉTON :

INFRASTRUCTURE :

- Ouvrages contre terre:	XA1	C30/37 (SIC sur plan)
- Dalles coulées en place :	XA1	C25/30 (SIC sur plan)
- Poutres en béton armé :	XA1	C25/30 (SIC sur plan)
- Voiles et poteaux :	XA1	C25/30 (SIC sur plan)
- Fondations, longrines ,Radiers :	XA1	C25/30 (SIC sur plan)

SUPERSTRUCTURE :

- Sous Sols (planchers Parking,rampe.poteaux poutres, voiles):	XC1	C20/25 (SIC sur plan)
- Balcons ,toitures terasses avec étanchéité et elements exposés:	XF1	C25/30(SIC sur plan)

FISSURATION:

Préjudiciable

· Par ailleurs, les règles particulières du DTU 14.1 s'appliquent pour tous les éléments faisant l'objet d'un cuvelage.

DEGRÉ COUPE FEU:

-Infrastructure: SF/CF 2H00
-Superstructure:
SF/CF 1H voiles et poteaux
SF/CF 1H dalles
SF/CF 2H locaux à risque élevé
SF/CF 2H gaines compris à la traversée des planchers

ENROBAGE:

-Ouvrages Contre-Terre: 4cm (max 5 cm pour cuvelage)
-Autres Ouvrages: 3cm

CONTRAINTE DE SOL :

-Semelle (à L'ELS): 3 bars
-Semelles provisoires (à L'ELS): 1.5 bars

PLANS DE RÉFÉRENCE:

-Plan Architecte: -- A03 P4- Plan R+1 / A04 P4- Plan R+2
-Plan Synthèse: --
-Coupes Coffrage: -- AES_EXE_BET_TZ_R+1_COF_0110-Coupes coffrage R+1

NOTA: - Les poids propres recharges/relevés/socles... sont à considérer selon dimensions sur plan , en plus des CP / CE plans de charges
Maconnerie Non Porteuse (MNP) : 1.35T/m3
Voile Non Porteur (VNP) : 2.5T/m3 (poids propre est pris en compte dans la charge permanente)

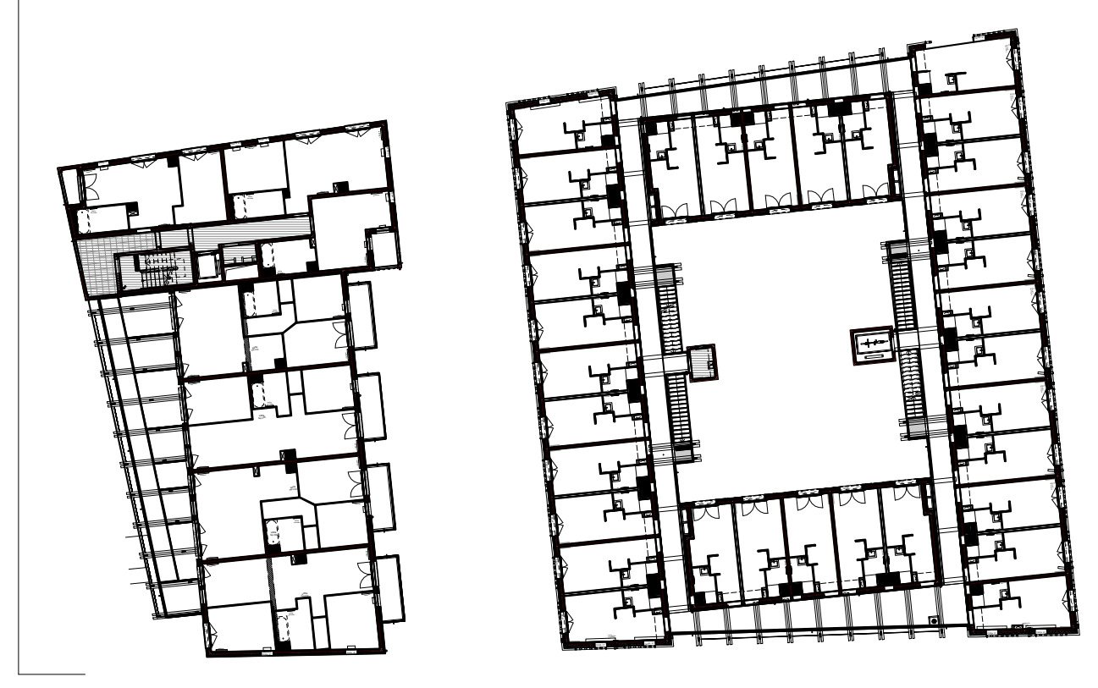

▦	CP = 100 daN/m² CE = 400 daN/m²
▤	CP = 100 daN/m² CE = 250 daN/m²
▨	CP = 100 daN/m² CE = 350 daN/m²
▦	CP = 100 daN/m² CE = 150 daN/m²

LÉGENDE

- PV : Poutre-voile
- V.N.P. : Voile non porteur
- M.N.P.: Maçonnerie non porteuse
- J.S.: Joint Sec
- J.D.: Joint de Dilatation
- J.F.: Joint de Fractionnement
- DPP.: dalle en prédalles précontraintes
- DP ou CSP. : dalle pleine coulée sur place
- DAP. : dalle alvéolaire
- P : Element Préfa
- PE : Element Préfa Evidée

} Ai dalle ou poutre
Matage

Dalle
Partie coulée avec la classe de béton renseignée

☐	Voile BA étage courant
▩	Paroi moulées VPP
▨	Voile en Prémur
▨	Voile BA étage supérieur
▩	Parpaing étage courant
▨	Parpaing étage supérieur
▩	Voile non porteur étage courant
▩	Voile BA étage supérieur non porteur
■	Poutre BA
- - - - - -	BN
C40/50	Classe de Béton de Poutre

Construction d'une résidence étudiante et de logements collectifs à Pierrefitte

LOTP4-Construction de 183 logements et parking en sous-sol
ZAC Brisais Pasteur_Pierrefitte-sur-Seine_Boulevard Pasteur

Constru[illegible]n d'une résidenc[illegible]étudiante et [illegible] logements acc[illegible]sion (183 lots)

13-21 boulevard Pasteur
93380 Pierrefitte-sur-Seine

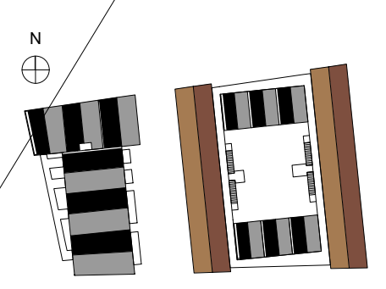

MAITRISE D'OUVRAGE
Bouygues Immobilier
1 rue du Parc à Charbon
93200 Saint Denis

ARCHITECTE
BFV Architectes
2, rue Labois Rouillon
75019 Paris

OPC
Cabinet TSB
3 allée des Gar[illegible]
91120 PALAIS[illegible]U

BET TCE structure - fluides
COTEC
[illegible]Rue des Grilles,
[illegible]00 Pantin

BET thermique & acoustique
RG Ingenierie
5 rue du Clos de l'Aumone
77184 Emerainville

CONTROLEUR technique & SPS
BTP Consultants
202 quai de Clichy
92110 Clichy

GEOTECH[illegible]CIEN
ROCSOL
30 bis, ru[illegible]'Estienne d'Or[illegible]
92120 [illegible]ouge

[illegible]O CERTIFICATION
[illegible]ardonnel
5, rue de la Mare à Tissier
91280 Saint Pierre du Perray

TZ
PHASE
EXE

BURE[illegible] ETUDES STRUCTURE EXE

AES
Bureau d'Etudes Techniques

AES-BET
[illegible]68, Avenue [illegible]aréchal JUIN
[illegible]0 Mant[illegible] La Jolie
Tél. [illegible]1 34 76 71 80/+33 (0)1 34 79 32
[illegible]ntact@aesbet.com

Ind[illegible]e	[illegible]ate	Etabli par	Modifications
A	22/10/2021	AES - M.R	Premièr[illegible] Diffusion
B	23/11/2021	AES - M.R	MAJ G[illegible]érale

TITRE [illegible]U PLAN	ECHELLE	TYPE	N° DOC	NIVEAU	ZONE	INDICE
Plan [illegible]rage PH R+1	1/50	COF	0100	R+1	TZ	B

EnCours 211123