Tél.
e-mail contact@bet-structuro.com

HOUILLES

Objet

CONSTRUCTION D'UNE MAISON
INDIVIDUELLE

Partie d'ouvrage

Maître d'ouvrage M. Pedro Navarro Arce

Dessin		échelle
1	Coffrages - Fondation	1/25

Ingénieur des structures	Conducteur des travaux
BET STRUCTURO	

Date 07/04/2026 Révision Mise à jour Protocole

Ce projet est protégé par la loi.

DISPOSITIONS CONSTRUCTIVES

Béton vibré, classe min C^{25}_{30}
Enrobage min = 3 cm

2 ou 4 Equerres d'angle horizontaux 60×60 – Ø 10 mm à prévoir au niveau des fondations, à chaque intersection de semelle


Intersection en L Intersection en T

2 ou 4 Equerres d'angle horizontaux 60×60 – Ø 10 mm à prévoir au niveau des fondations, à chaque intersection de chainage horizontal

Intersection en L Intersection en T


4 Equerres verticaux 60×60 – Ø 10 mm, à prévoir au niveau des fondations, à chaque poteau ou chainage vertical

U verticaux 16cm×H – Ø 10 mm – espace. = 16.5 cm ancrés dans la fondation à prévoir au niveau des murs de soubassement

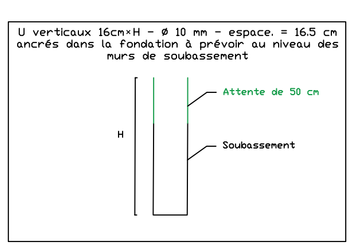

FONDATION

Assise semelle ou gros béton = 1.30 m minimum /Niveau fini et également /TN

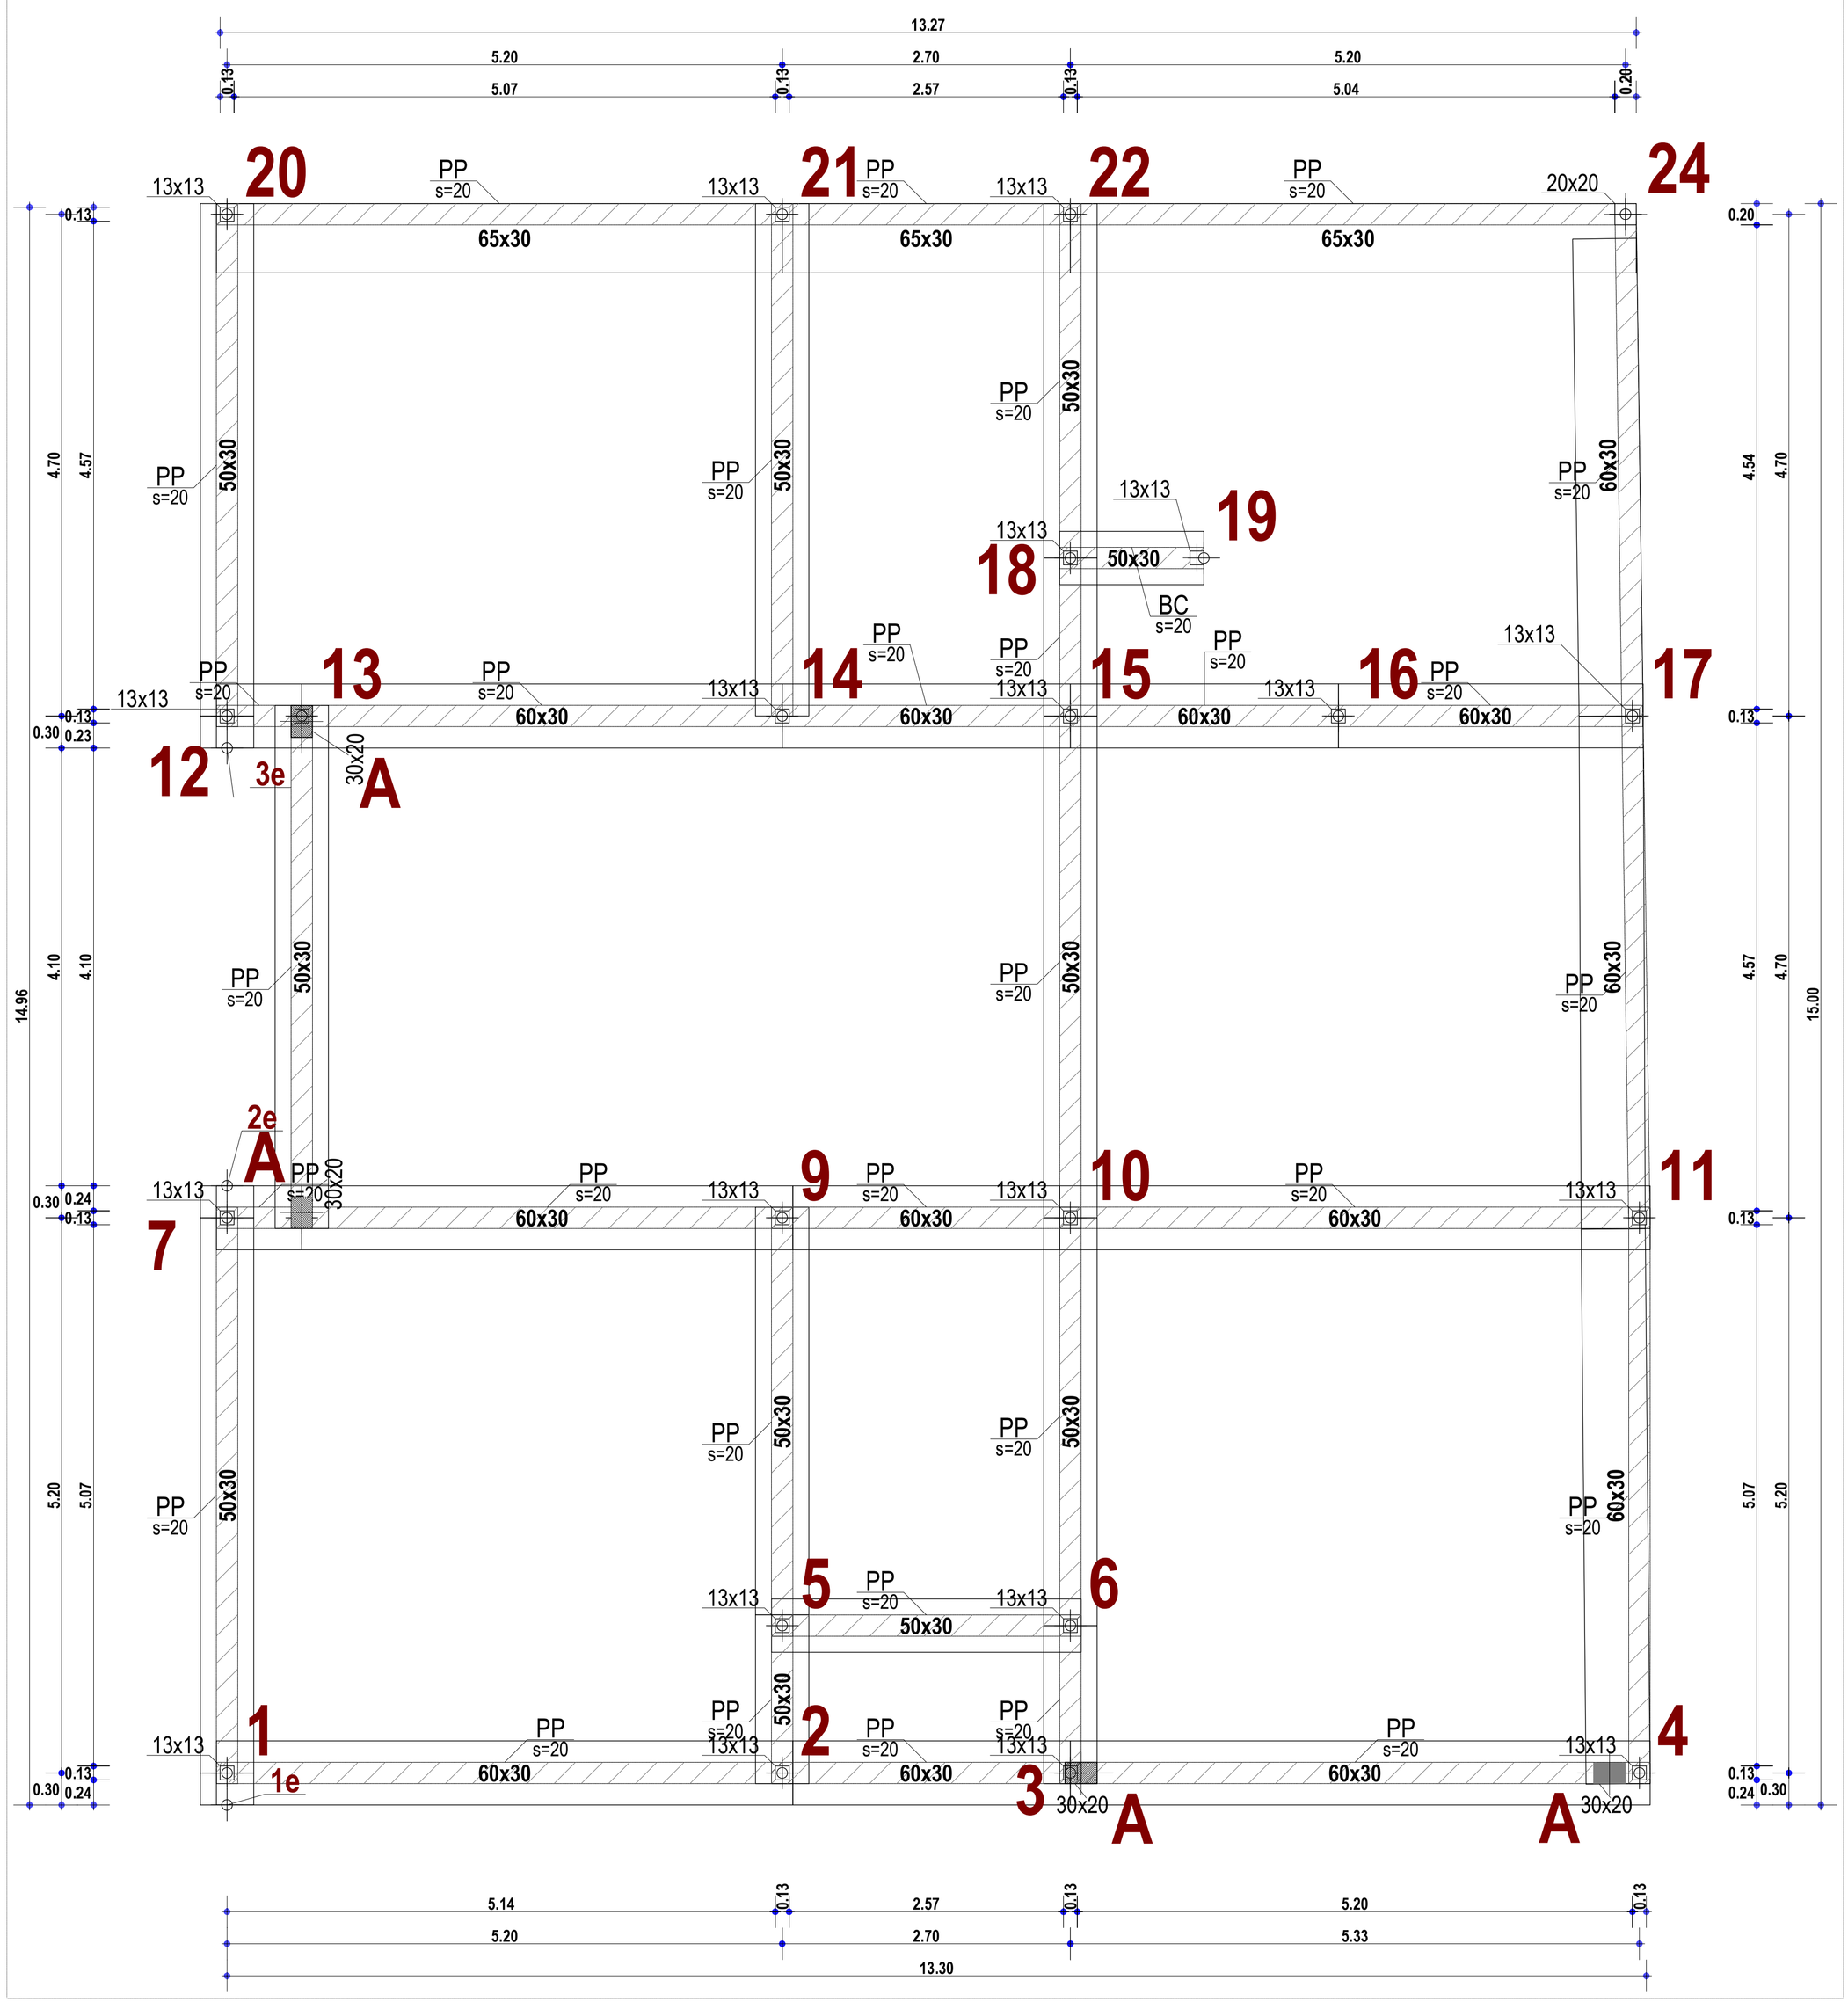

Échelle: 1/25