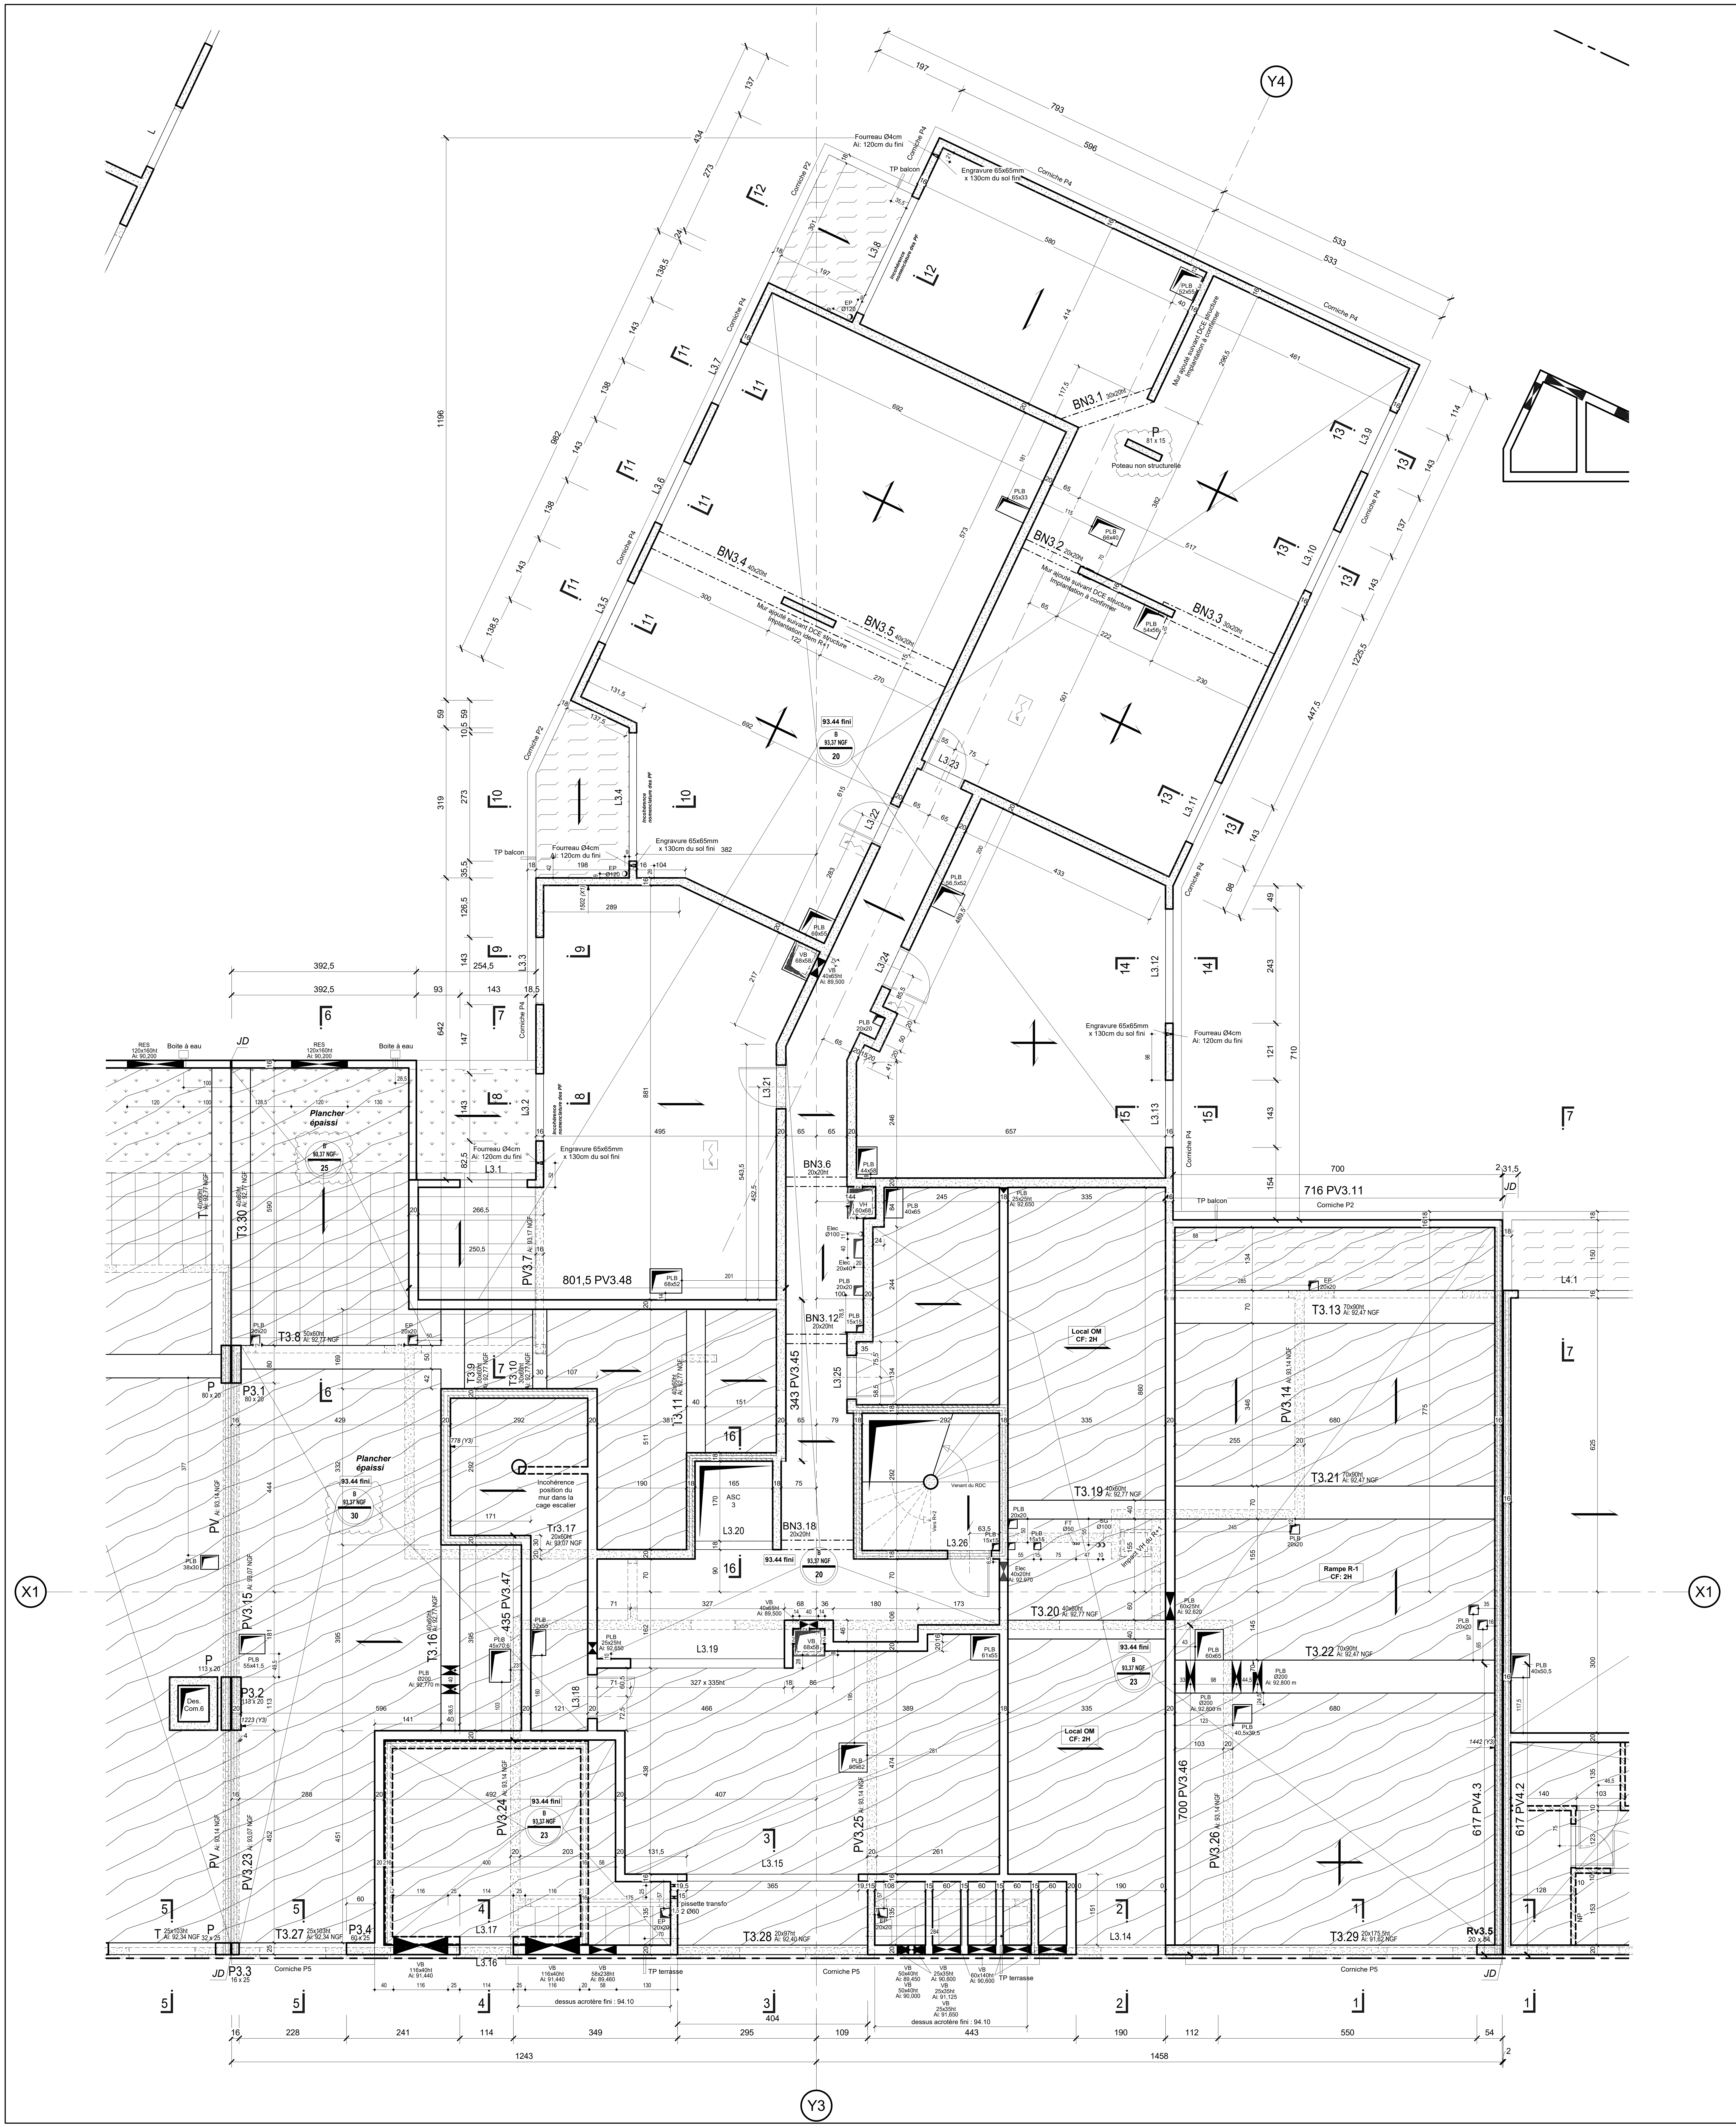

PLANS DE REFERENCE

CORPS D'ETATS	LOT	Entreprise	Intitulé du plan	Indice	Date	Reçu le
	Architecte	Selas François de Alexandris	Dossier marché	-	13/07/2022	14/02/2022
	Etanchéité	-	-	-	-	-
	Menuiserie int.	-	-	-	-	-
	Menuiserie ext.	Ateliers de Beauce	Coupes de principe	-	-	-
	Electricité	A.L.GOMES	Cahier de gaines techniques	-	-	-
	Plomberie	-	-	-	-	-
	Ascenseur	OTIS	Plan d'installation et de réservations	0	21/12/21	-
	Chape	ALBUQUERQUE	Réservation + localisations chapes	-	-	-
	Serrurerie	-	-	-	-	-

Etude effectuée suivant les plans ci-dessus

▨ Isolant sous dalle

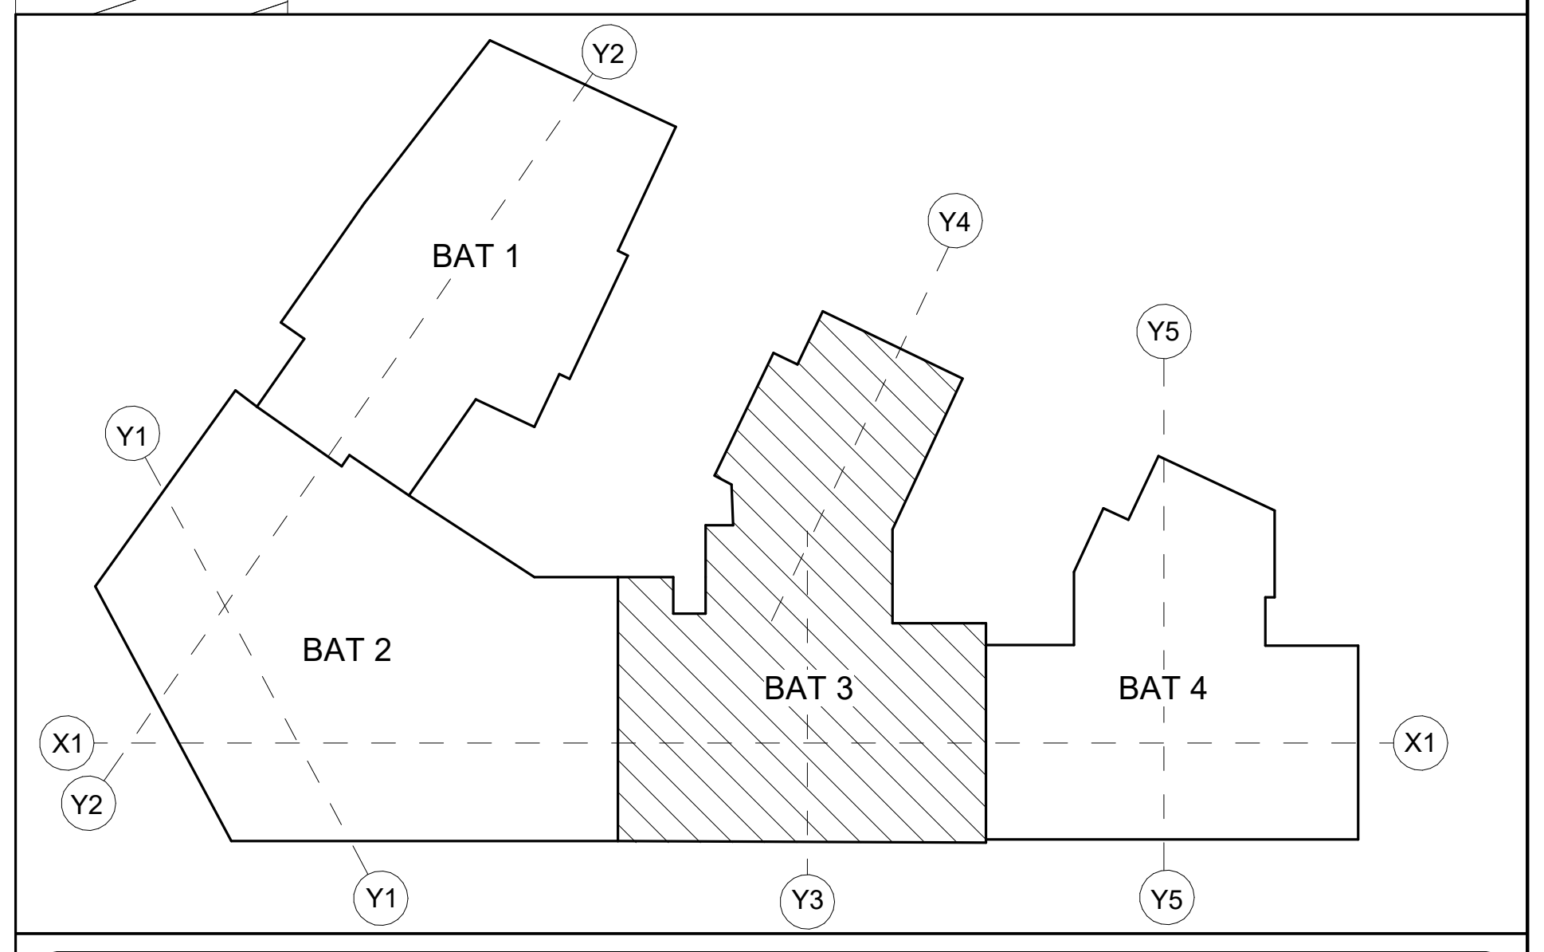

INDICATIONS

Divers :

Neige zone 1A altitude inf. 200m
Vent zone 2 site normal
Sismicité zone 1 catégorie II

Sauf indication contraire sur plan

Classe d'exposition :

- Intérieur : XC1 / Enr. mini 3cm
- Extérieur : XC4 / Enr. mini 4 cm
- Fondation : XC2 / Enr. mini 3.5 cm

Aciers : Fyk = 500 MPa
Béton : Fck = 25 MPa

Sauf indication contraire sur plan

Stabilité au feu :

Dalles : 1H
Poutres : 1H
Verticaux : 1H

Sauf indication contraire sur plan

Charge réparties	ZONE / N°	Charges permanentes kg/m²	Charges d'exploitation kg/m²
	Logements	190	150
	Circulation	100	250
	Balcon	150	350
	Terrasse accessible	120	250
	Terrasse inaccessible	100	100
	Terrasse végétalisée	1000 (50cm de terre)	250
	...	...	...
	...	...	...

Sauf indication contraire sur plan / Charges de poids propre non comprises

☐	Béton
▨	Agglos plein
▨	Agglos creux
▒	Impact voile supérieur
PV	Poutre Voile
VPP	Voile par passe
T	Poutre
Tc	Poutre en console
Tr	Poutre relevé
P	Poteau
V	Voile
Lg	Longrines
L	Linteau
BN	Bande noyée
S	Semelle isolée
SF	Semelle filante
Px	Pieux
Att	Attentes
R	Raidisseur vertical
CH	Chaînage horizontal
All	Allège
Ai	Arase Inférieure
As	Arase Supérieure

NOTA :
- Les murs sont stabilisés en tête par la charpente
- Ne pas oublier de crosser ou capuchonner toutes les attentes verticales
- Hors mission : méthodologie entreprise et étude de sol

NIVEAU DE REFERENCE : ±0,00 = ...,.. NGF

61, Rue d'Enfer
02000 LAON
2, Rue Louis de Broglie
59260 LEZENNES
03 23 27 12 90
begt@begt.fr
www.begt.fr

BEGT
ÉTUDES TECHNIQUES DE STRUCTURES DU BÂTIMENT

OPQIBI L'INGÉNIERIE QUALIFIÉE CERTIFICAT N° 13 04 2562

92150 SURESNES

Cst de bâtiments de logements et commerces

1-15 rue du Dr Marc Bombiger 2-6 avenue Jean Jaurès

Architectes :
SELAS FRANCOIS DE ALEXANDRIS
10, rue Général Castelnau
75015 Paris

Maître d'Ouvrage :
SCI Résidences franco suisse
138-140, avenue Aristide Briand
92160 ANTONY

Entreprise :
BJF SAS
59 Rue du Tir
77500 CHELLES

Bureau de contrôle :
BTP Consultants
19, Avenue du Centre
78280 Guyancourt

PH RDC
Vue en plan
Bâtiment 3

Affaire : J206-10-22
Calculé par : Q. MERVEILLIE
Dessiné par : L. MATHIS

EXE	Echelle	Lot	Zone	Niveau	Numéro	Indice	Date 1er envoi
	1 : 50	GO -	B3 -	R0 -	100	C	17/02/2023

Indice	Modifications	Date
0	1ère Diffusion	17/02/2023
A	MAJ générale	24/02/2023
B	Mises à jour suivant CES et CET, suivant visas MOE et entreprise de GO, repérage des bandeaux, des acrotères	02/06/2023
C	Mises à jour suivant calculs de structure	09/06/2023

NOTA :
Sans notification contradictoire des corps d'états et intervenants sous 15 jours, les plans seront réputés bon pour exécution
Ce document est la propriété du BEGT. Il ne doit pas être reproduit, utilisé ou communiqué à un tiers sans autorisation écrite préalabe.